




EVENT HORIZON HOUSE

A HOME BETWEEN TIME & INFINITY

A Mobius Loop structure rests on the stable ring of a black hole's event horizon. The house exists where time bends, allowing a family of four to live in a different rhythm within the same infinity.

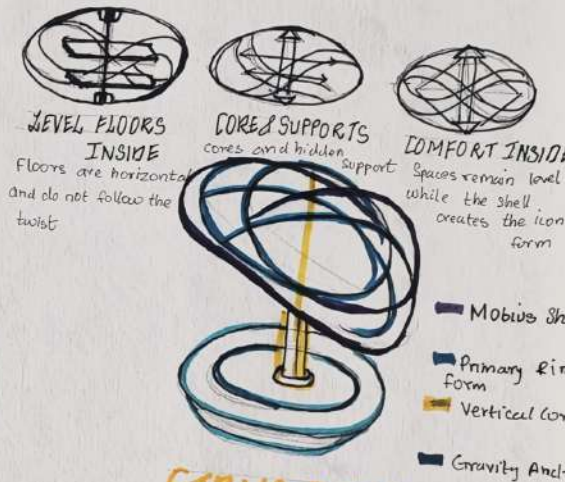

A DAY IN THE LIFE

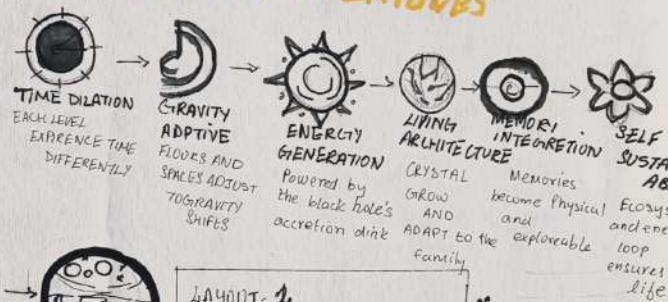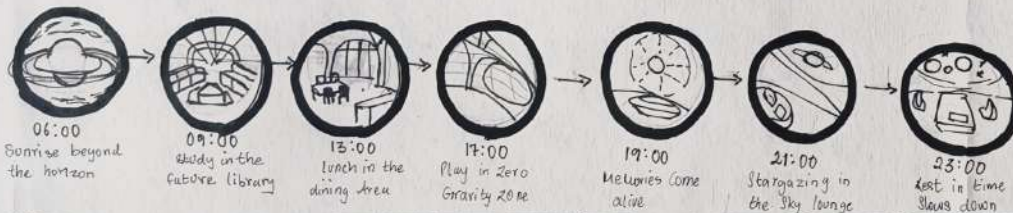


LAYOUT 1

CONCEPT & FUNCTIONS

MINIPLO: TUN - BE-IND-0177

"We do not live in this house.
We live between moments."

KEY CONTEXT DIAGRAM

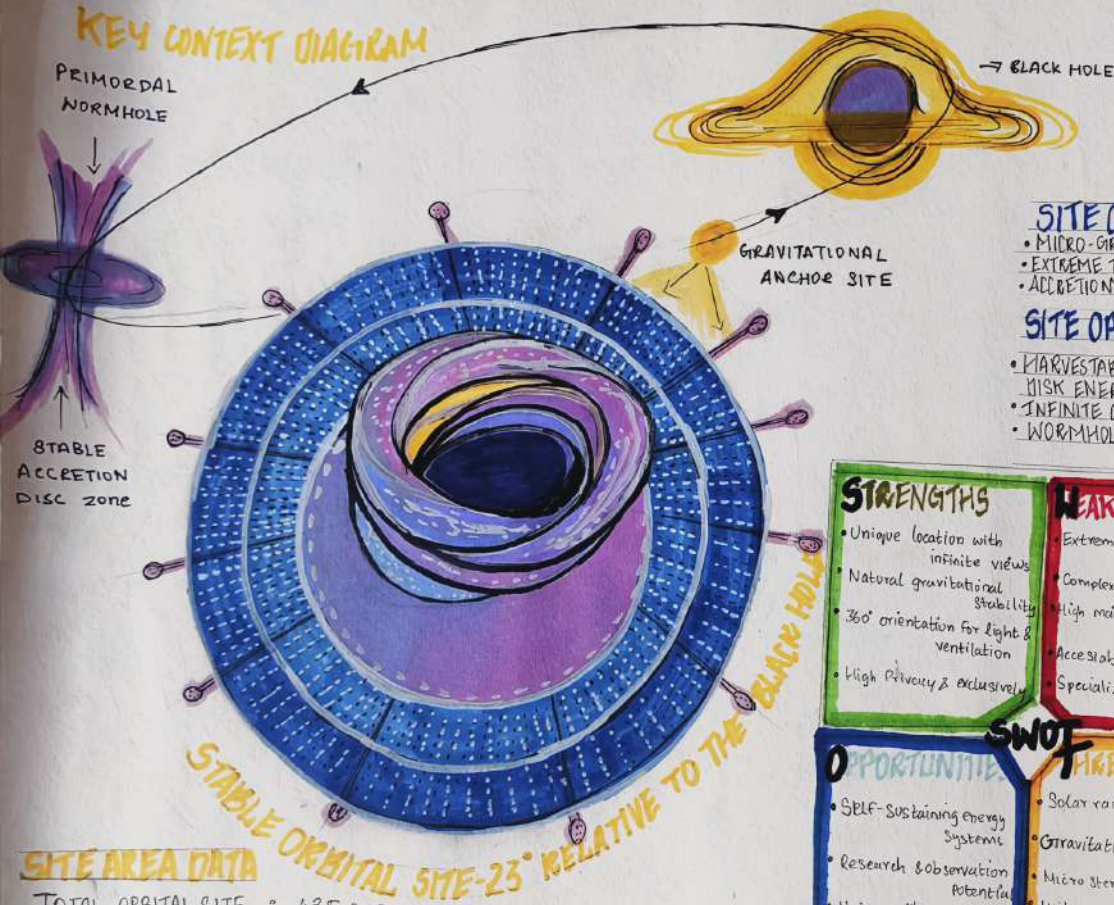

SITE CONDITIONS

- MICRO-GRAVITY ZONE
- EXTREME TIDAL FORCES
- ACCRETION DISK LUMINOSITY

SITE OPPORTUNITIES

- HARVESTABLE ALTERATION
- RISK ENERGY
- INFINITE COSMIC VIEWS
- WORMHOLE ACCESS

STRENGTHS

- Unique location with infinite views
- Natural gravitational stability
- 360° orientation for light & ventilation
- High privacy & exclusivity

WEAKNESSES

- Extreme environment conditions
- Complex structural engineering
- High maintenance and energy need
- Accessibility challenges
- Specialized material requirements

OPPORTUNITIES

- Self-sustaining energy systems
- Research & observation potential
- Unique living experience
- Potential for futuristic technologies

THREATS

- Solar radiation & cosmic storms
- Gravitational fluctuations
- Micro-steroid impacts
- High complexity
- Dependence on advanced technology

SITE AREA DATA

TOTAL ORBITAL SITE : 435,000 sqm

GRAVITATIONAL ANCHOR FIELD : 110,000 sqm

MORBUS LOOP BUILDING : 8,000 sqm

TOTAL UNRESTRICTED AREA : 15,000 sqm

MINDIO: TUB-A-3-2NO-0197

SITE ANALYSIS AND SITE PLAN LAYOUT-1

COMETITION ENTRY FOR MR AND MRS VANCE

SITE ENVIRONMENTAL ANALYSIS

1 ENVIRONMENTAL FORCES




2 STABILITY ANALYSIS



3 ATMOSPHERIC AND ZONING




4 SITE ACCESS AND LOGISTICS

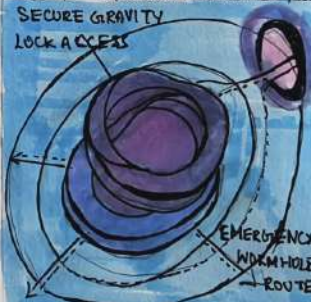


EVENT HORIZON HOUSE- PLAN LAYOUT

CLIENT- MR&MRS. VANICE

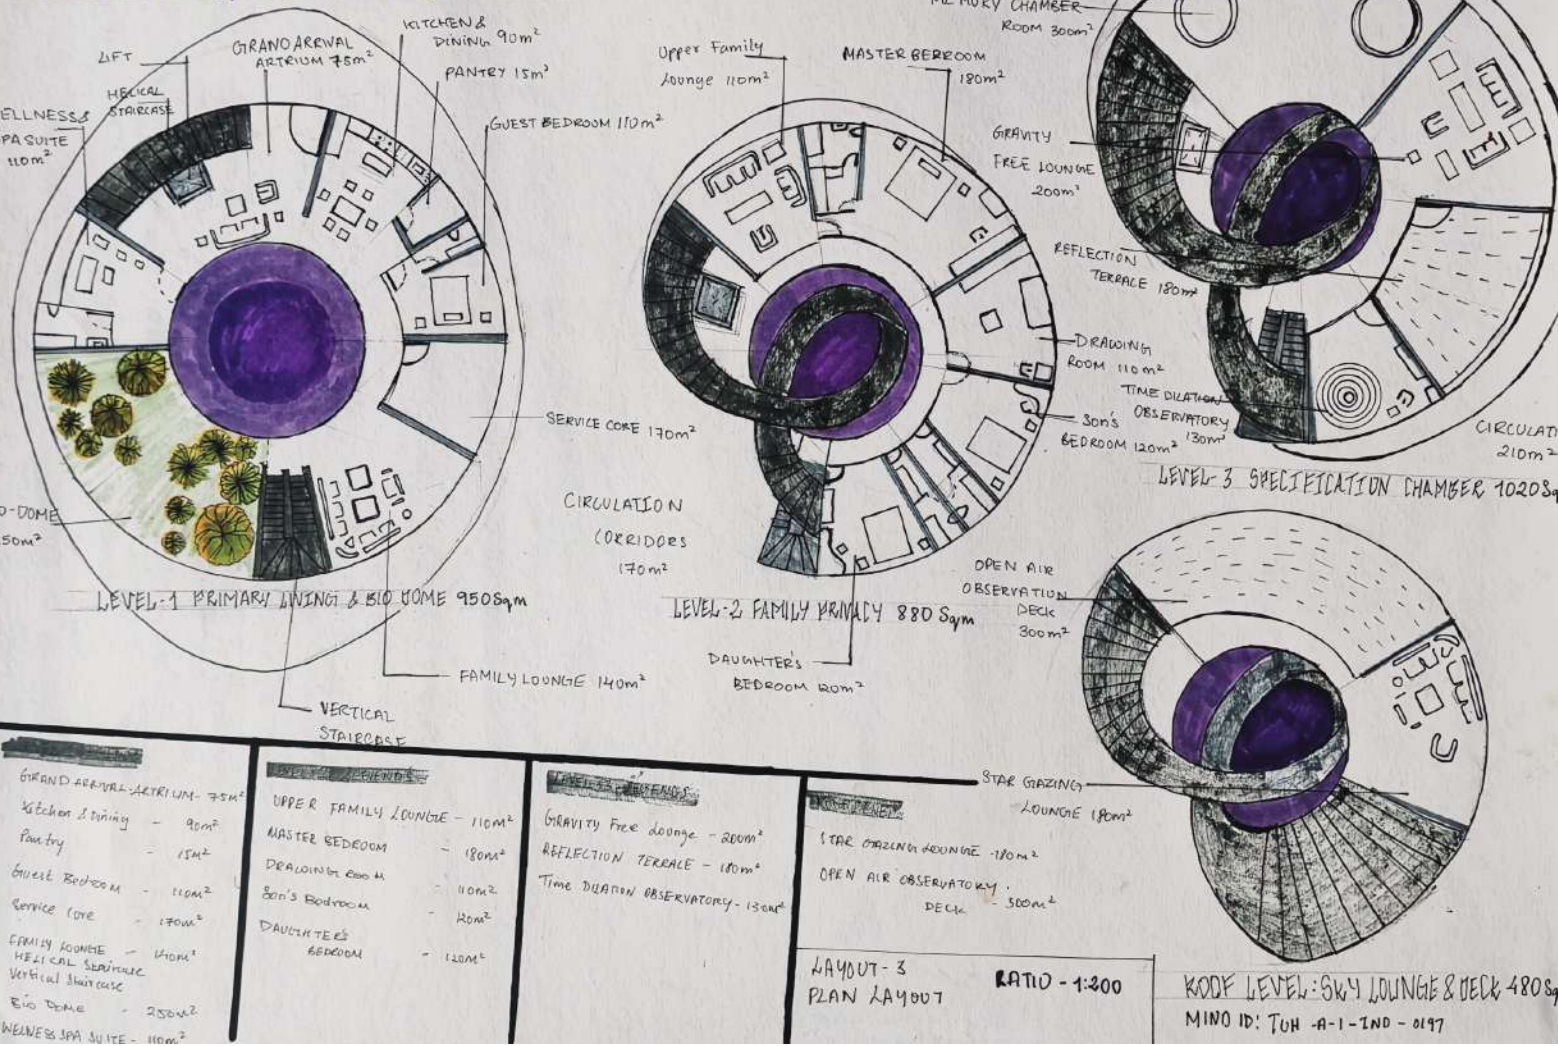


ELEVATION & SECTION - PHYSICAL STRUCTURE

NORTH-EAST EXTERIOR ELEVATION - Y-Y

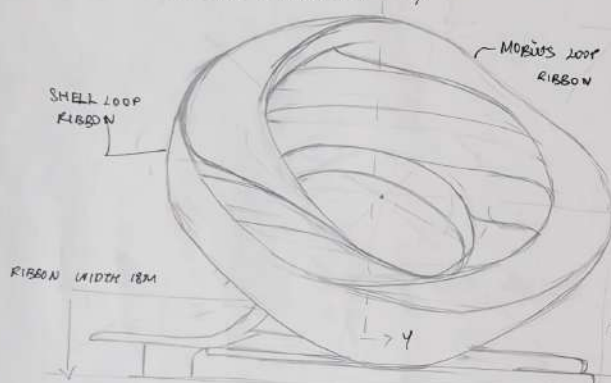


FULL HEIGHT VERTICAL SECTION - Y-Y

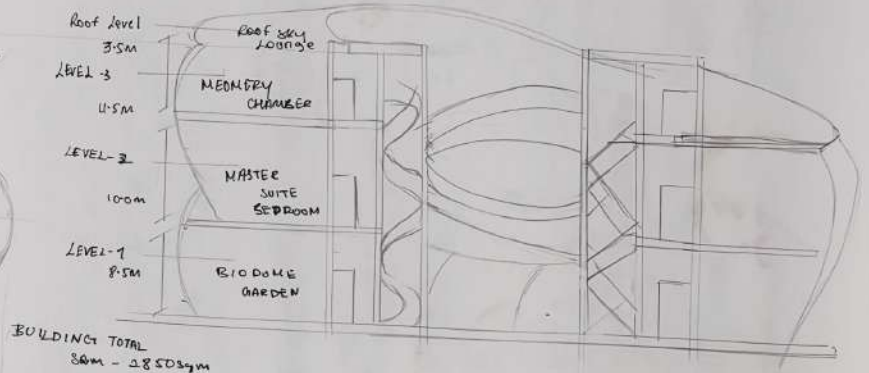


SOUTH-WEST EXTERIOR EXTENSION

CURVATURE RADIUS - 55M

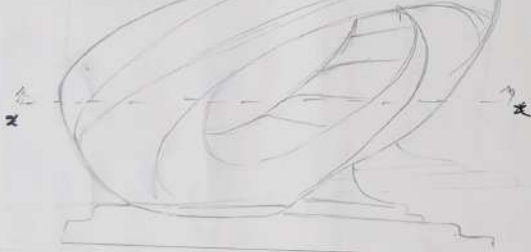

Longitudinal Section X-X

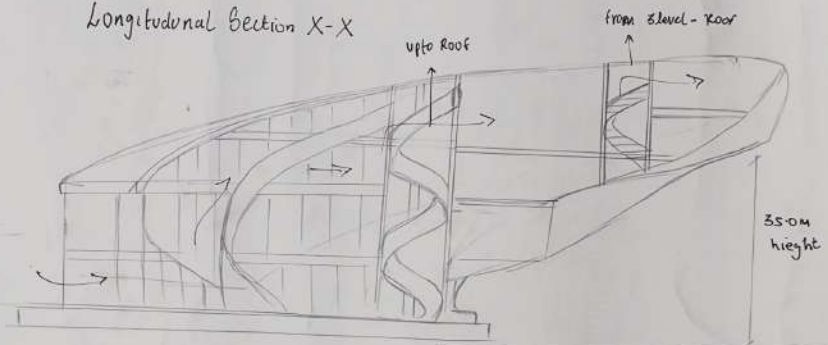

LAYOUT-4 MINDIO: TWH-A-I-IND-0197

ELEVATION & SECTION

RATIO: 1:200