




DR. VANCE: THE SCIENTIST AND DREAMER, FASCINATED WITH THE BLACKHOLE AND WANTING TO STUDY IT FROM CLOSE.



WHAT SEEMED AN OUTLANDISH THOUGHT WAS APPROVED AS AN IDEA THAT WAS REVOLUTIONARY

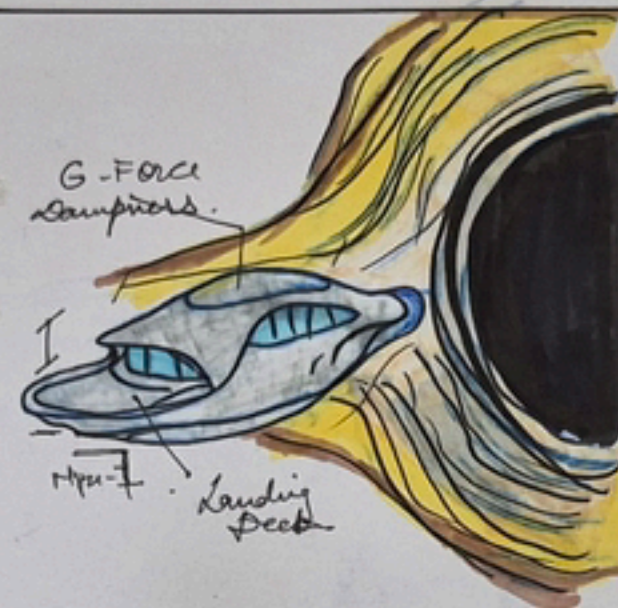

A HOME DESIGNED TO ANCHOR AT THE EDGE OF NYX-7



THE VANCE FAMILY REFUSED TO LET HIM GO ALONE, SO THEY DECIDED TO JOIN THIS VENTURE



THE PERILOUS JOURNEY: THREADING THROUGH DISTORTED LIGHT.



ARRIVAL: THE WALLS WITHSTOOD THE SPACE-TIME PULL



MR. VANCE SET UP HIS LABORATORY WHILE MRS. VANCE FOUND HER CANVAS.

ARCHITECTURE THAT ORBITS.
LIFE THAT ADAPTS.

CONCEPT: THE VANCE HOUSE IS A HOME SUSPENDED AT THE EDGE OF BLACKHOLE, WHERE TIME SLOWS, GRAVITY BENDS. ORBITING THE EVENT HORIZON OF A BLACKHOLE, IT TRANSFORMS ONE OF THE COSMOS MOST POWERFUL FORCES INTO A PLACE OF SHELTER, DISCOVERY AND BELONGING. DESIGNED FOR A FAMILY OF EXPLORERS, THE HOUSE IS MORE THAN A RESIDENCE - IT IS A SANCTUARY WHERE SCIENCE MEETS EMOTIONS.

SITE CONTEXT: THE SITE IS NOT A PIECE OF LAND BUT A GRAVITATIONAL TERRITORY. THE VANCE HOUSE IS LOCATED IN A STABLE ORBITAL PATH AROUND THE EVENT HORIZON OF A SUPERMASSIVE BLACK HOLE. THE SITE OFFERS UNPARALLELED COSMIC VIEWS AND A UNIQUE RELATIONSHIP BETWEEN ARCHITECTURE AND TIME. THE HOUSE EXISTS IN A DELICATE EQUILIBRIUM BETWEEN THE INFINITE PULL OF THE EVENT HORIZON AND THE HUMAN NEED FOR A HABITABLE, MEANINGFUL HOME.

DESIGN PRINCIPLES:



EMBRACE GRAVITY



TIME & MOTION




SELF-SUSTAINING



CONNECTED TO COSMOS

WATER & VEGETATION: NO NATURAL WATER OR VEGETATION EXISTS. EVERYTHING IS GENERATED AND RECYCLED.

WATER CYCLE

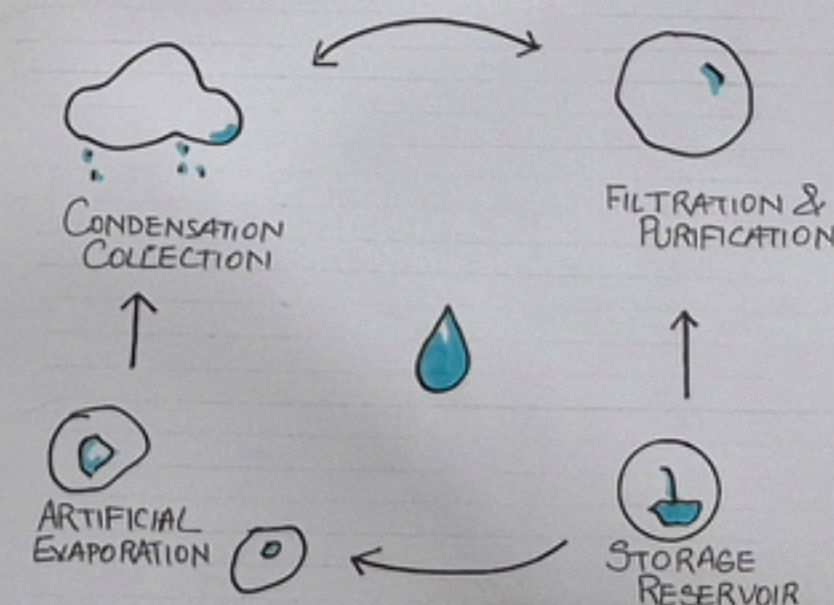


VEGETATION SYSTEM



ARTIFICIAL SUNLIGHT



HYDROPONIC SYSTEMS

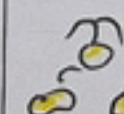


NUTRIENT RECYCLING




OXYGEN PRODUCTION


FORM DEVELOPMENT

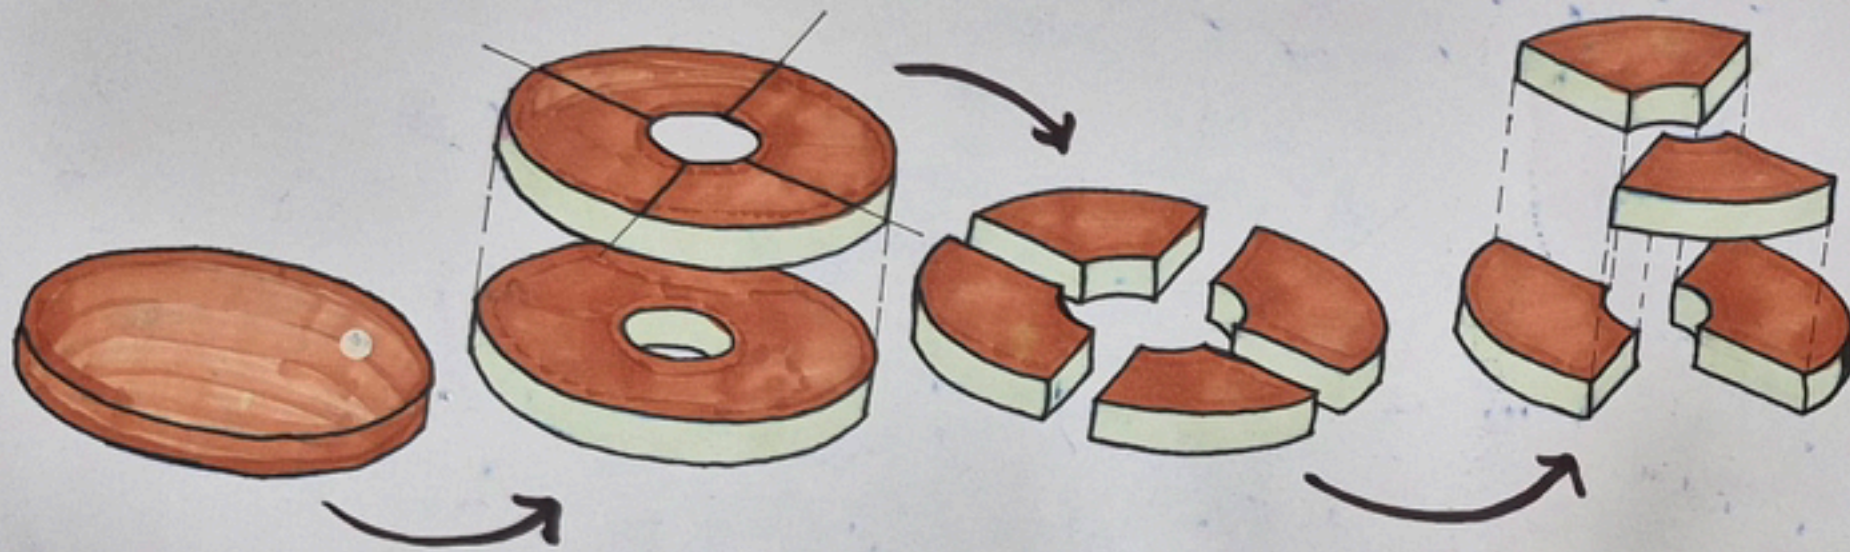


A SOLID CIRCLE TRANSFORMS INTO A RING WITH A CENTRAL VOID, DIVIDED INTO FOUR FUNCTIONAL ZONES AND STAGGERED VERTICALLY TO IMPROVE LIGHT, VENTILATION AND VIEWS.

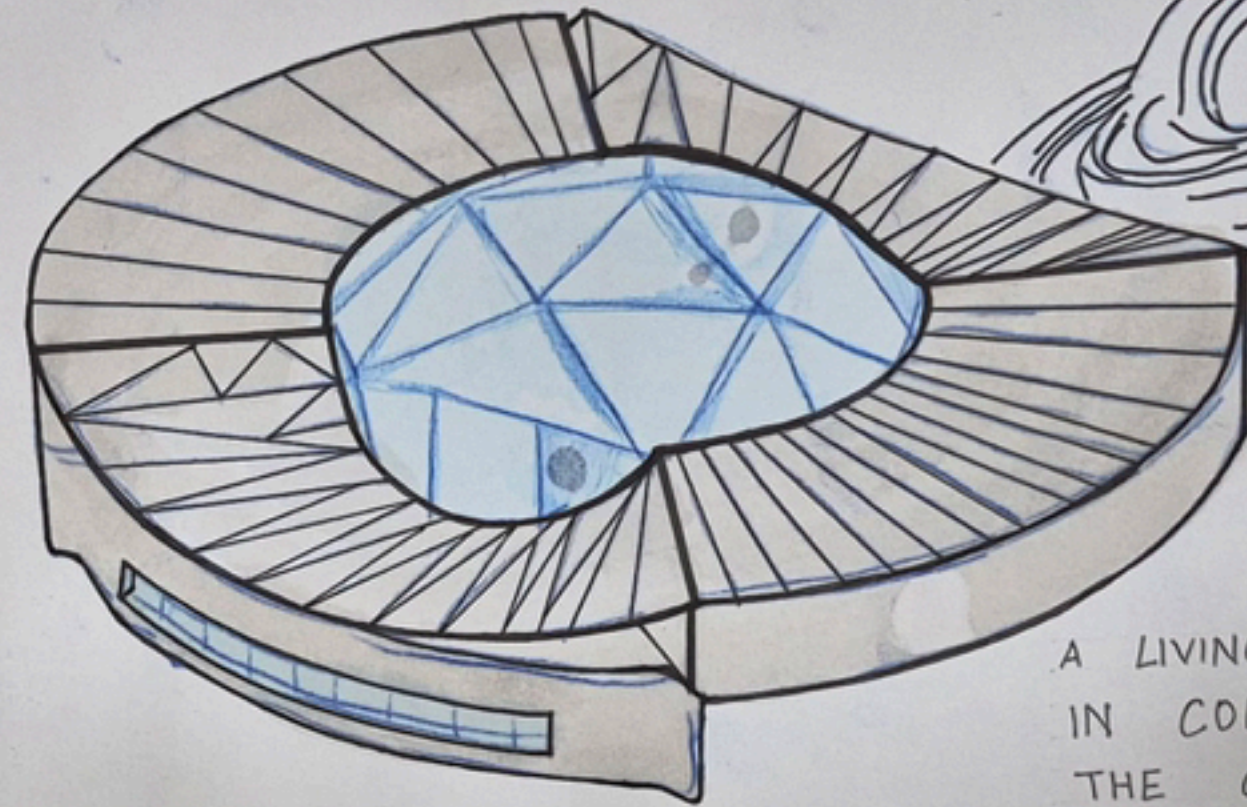


A LIVING EXPERIMENT IN COEXISTING WITH THE COSMOS.

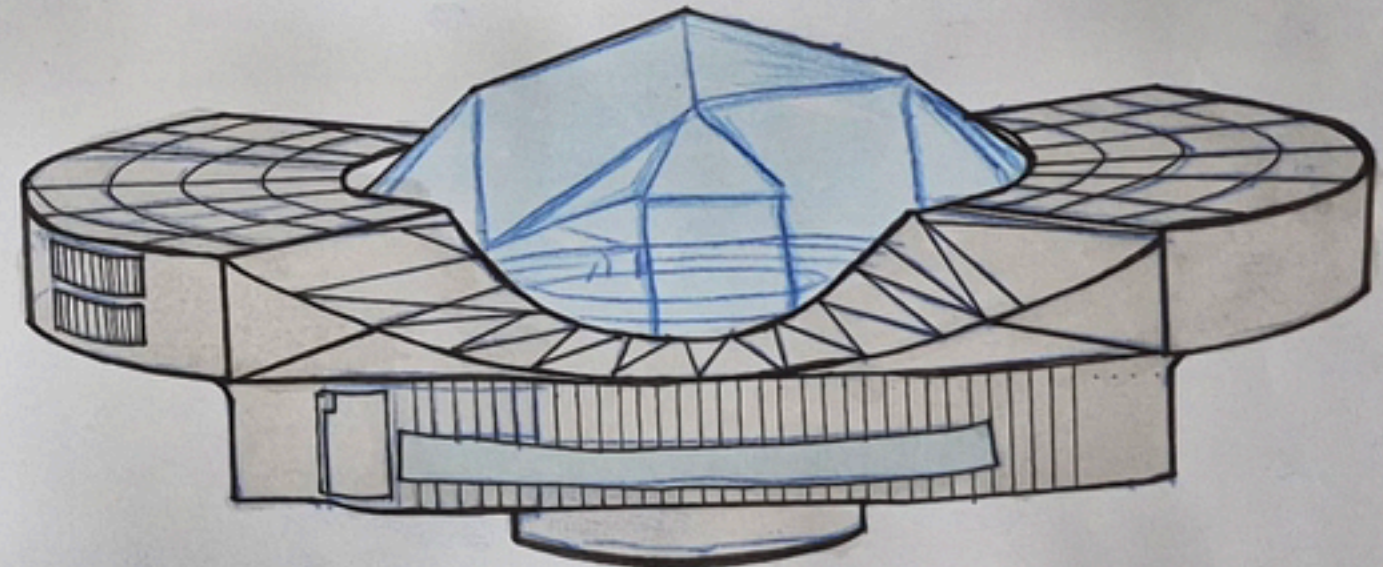

ELEVATION

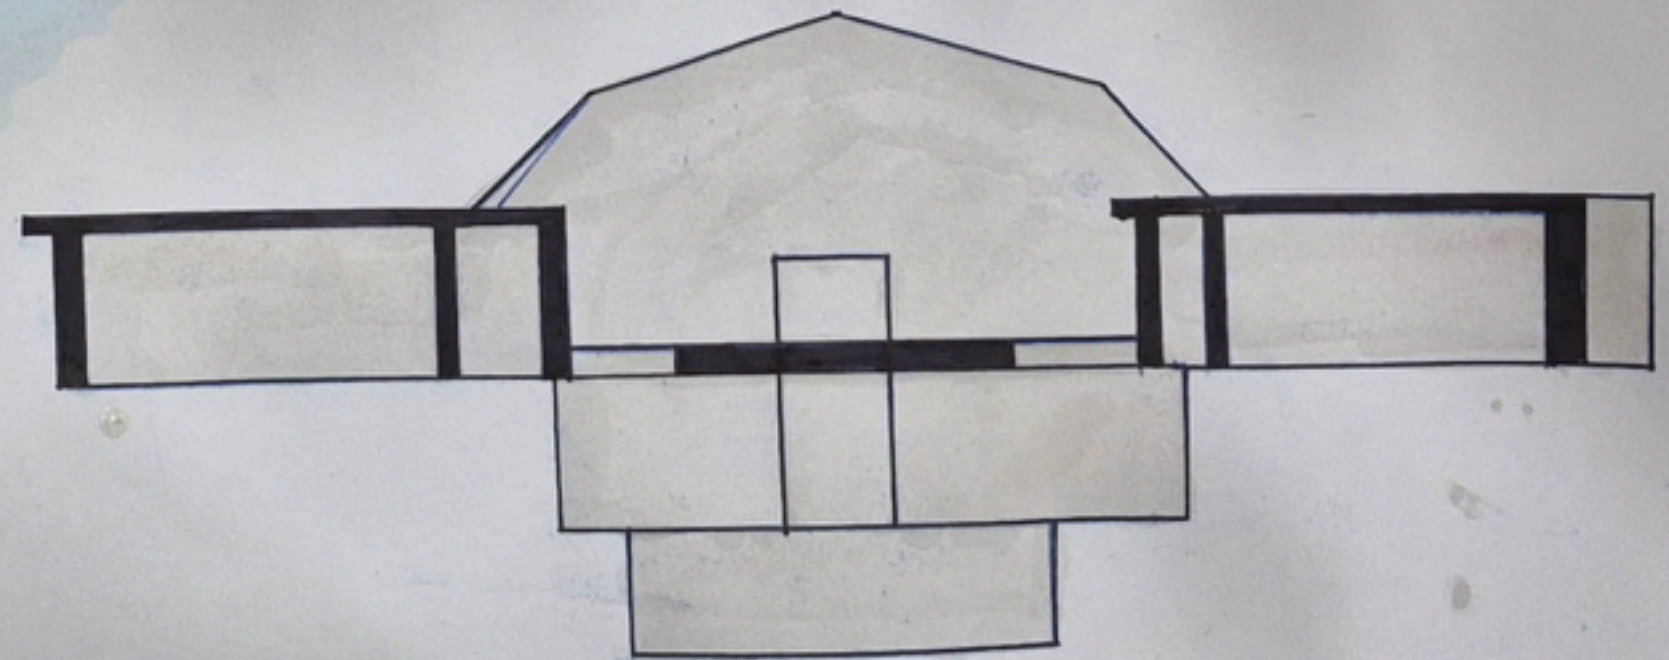


SECTION

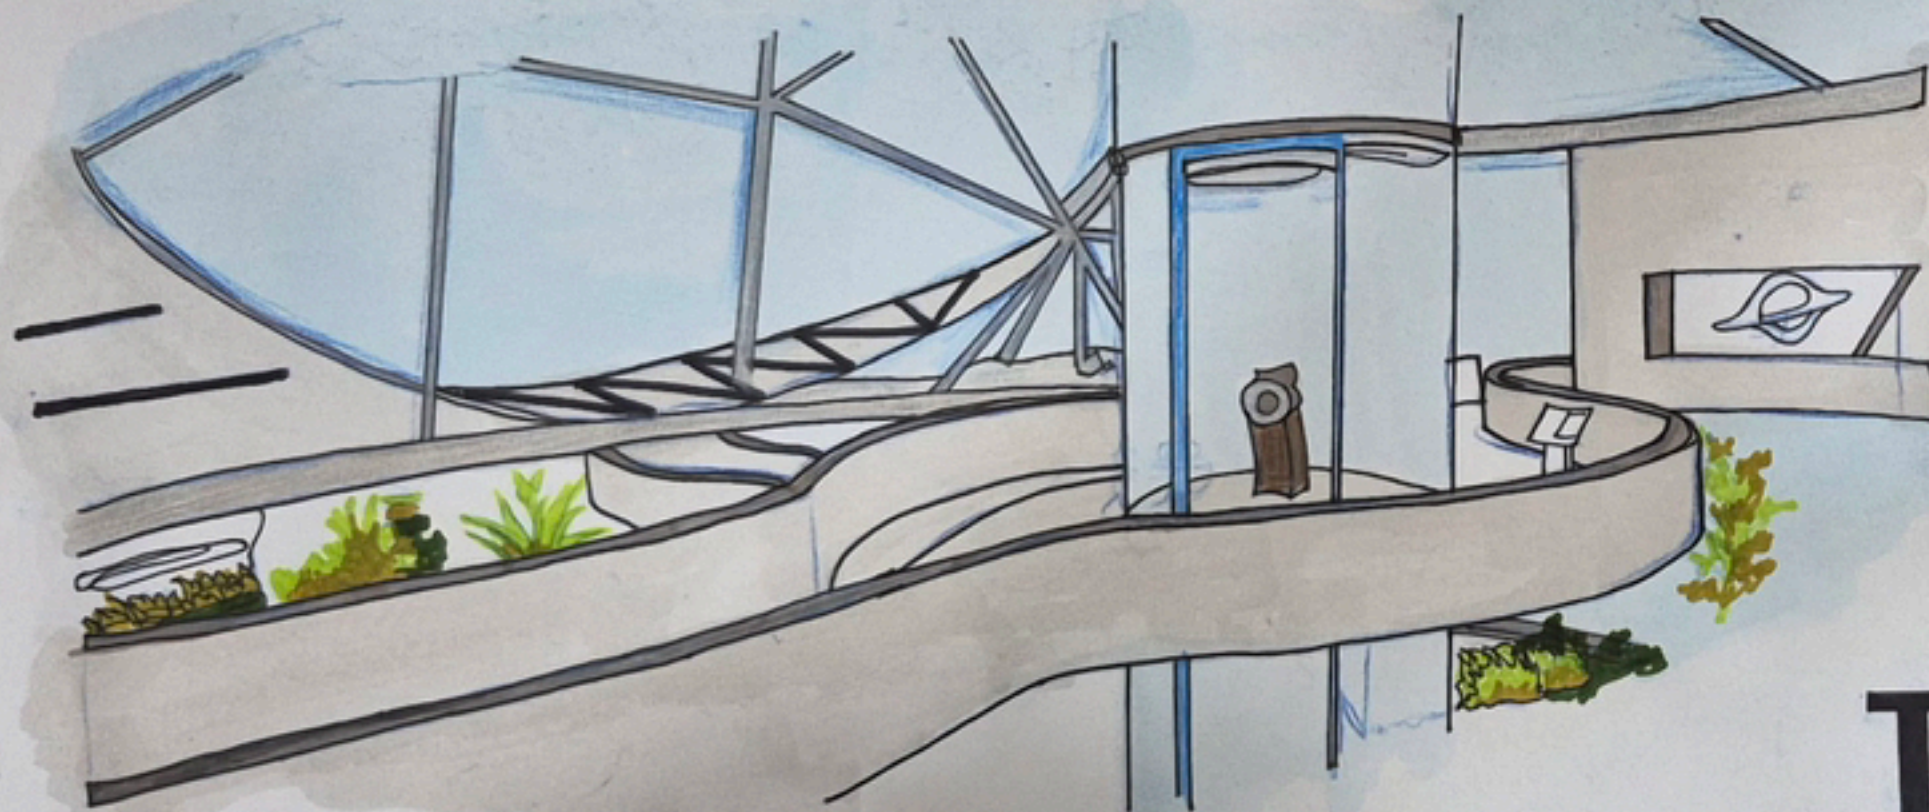

SKYWALK VIEW

THE SKYWALK OFFERS A FUTURISTIC ELEVATED PATHWAY THAT PROVIDES PANORAMIC VIEWS AND A UNIQUE APPROACH TO THE EVENT HORIZON RESIDENCE



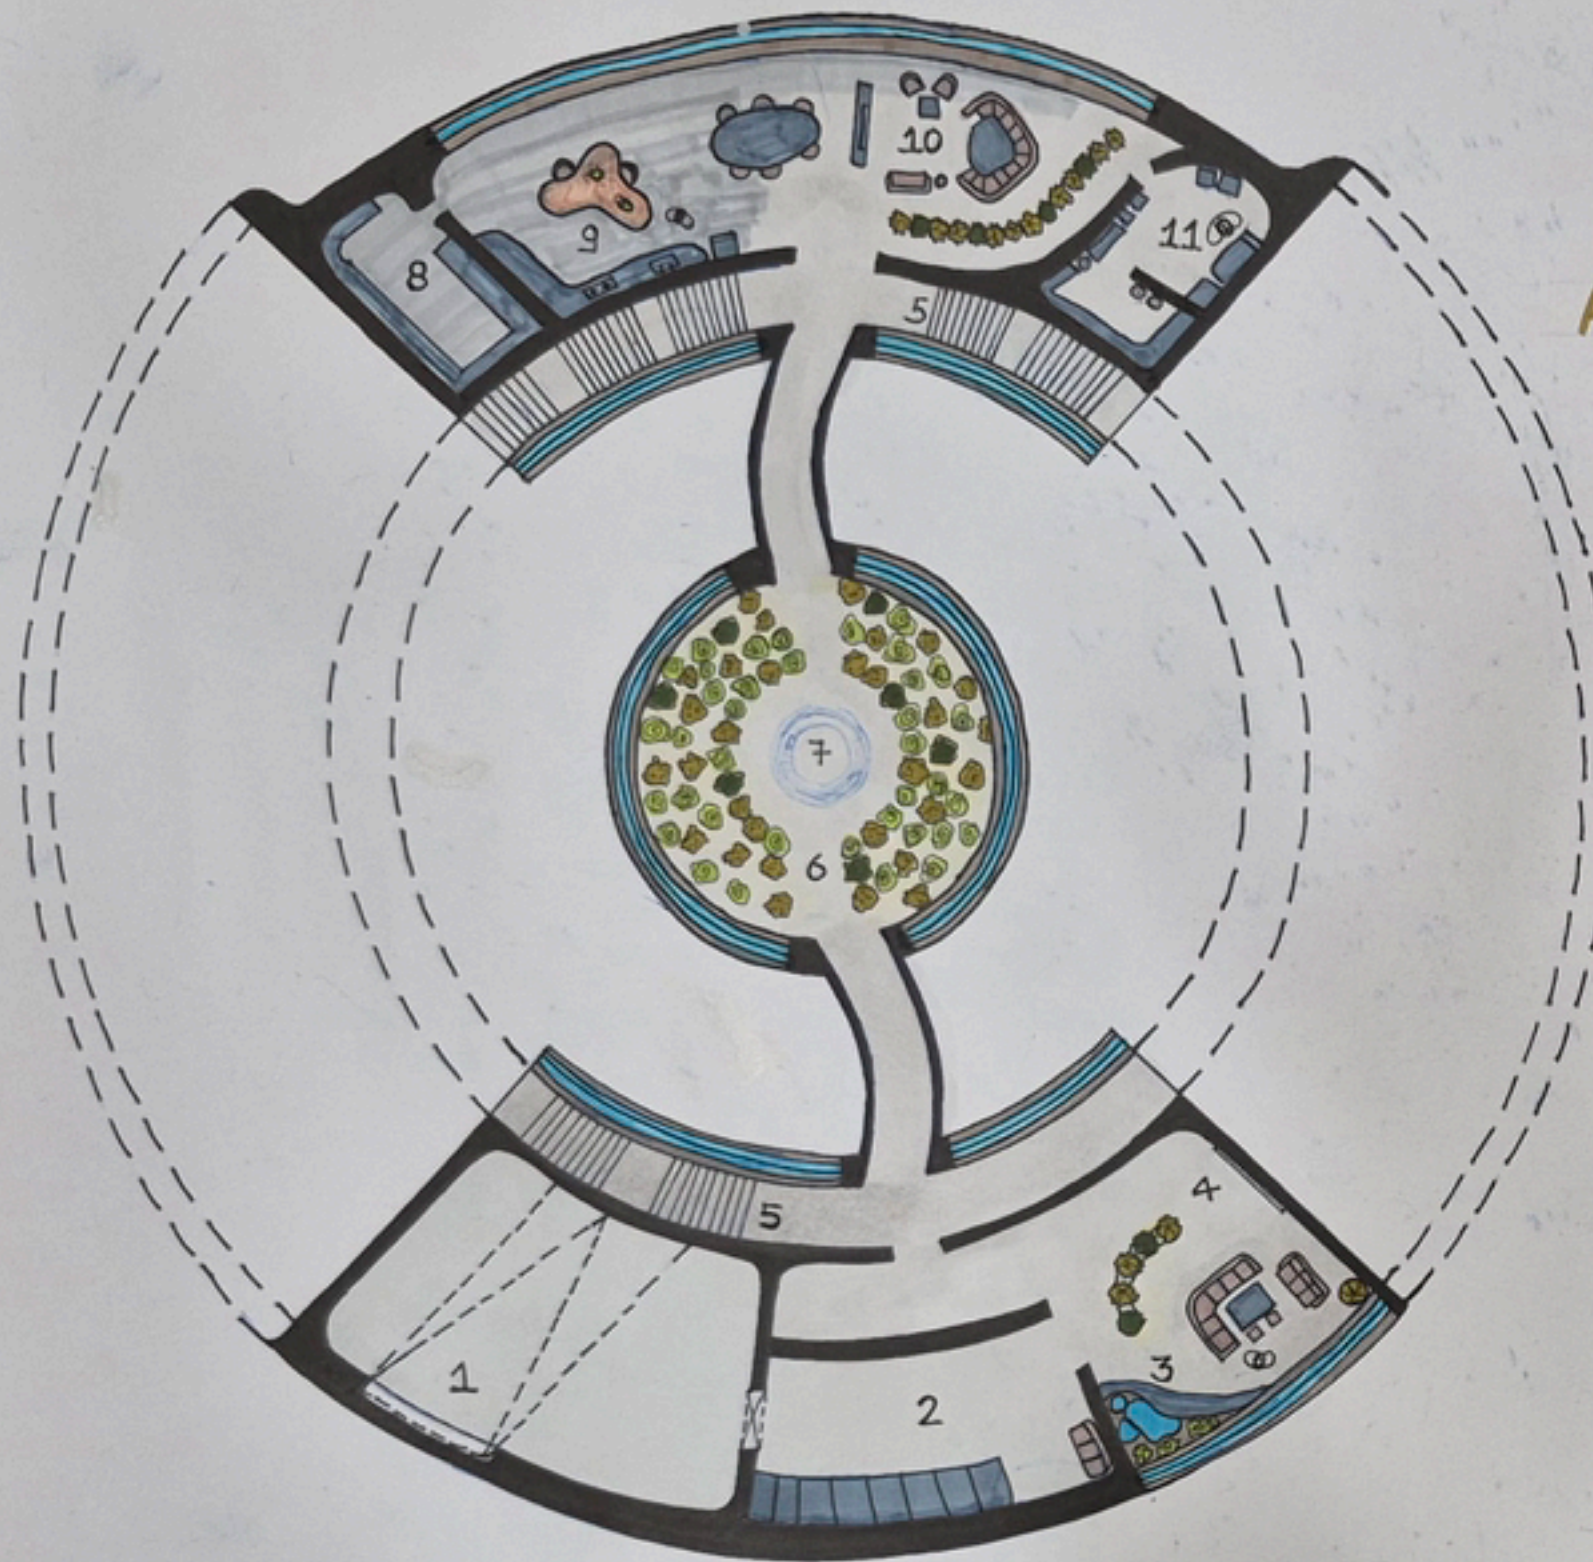

GROUND-FLOOR PLAN

- 1) DOCKING ZONE 12.8m x 8.7m
- 2) SPACE SUIT RACKS 10.9 x 5.5m
- 3) INTERIOR POND
- 4) DRAWING ROOM 8.9 x 8.7m
- 5) STAIRS
- 6) ARBORETUM rad: 6m
- 7) LIFT rad: 1.6m
- 8) FOOD STORAGE 3.5m x 6.8m
- 9) KITCHEN
- 10) LIVING ROOM
- 11) LAUNDRY/STORAGE 6.8m x 4.2m

ACCESS SEQUENCE


- APPROACH IN SPACECRAFT
- DOCKING AT ARRIVAL BAY
- AIRLOCK ENTRY
- TRANSITION CHAMBER
- INTO THE HOUSE



BASEMENT - MACHINE ROOM

- 12) SKYWALK 2m wide
- 13) MOTHER'S STUDIO 8.7 x 7.7m
- 14) PARENTS BEDROOM 8.3 x 8.7m
- 15) CONTROL ROOM 8.7 x 2.5m
- 16) MR. YANCE STUDY 8.7 x 9.4m
- 17) SON'S BEDROOM 8.6 x 9.3m
- 18) GYM 5.8 x 2.7m
- 19) GAMING ROOM 5.3 x 2.7m
- 20) DAUGHTER'S BEDROOM 8.6 x 9.6m

MAIN WALLS 0.8m THICK
INTERIOR WALLS 0.5m THICK

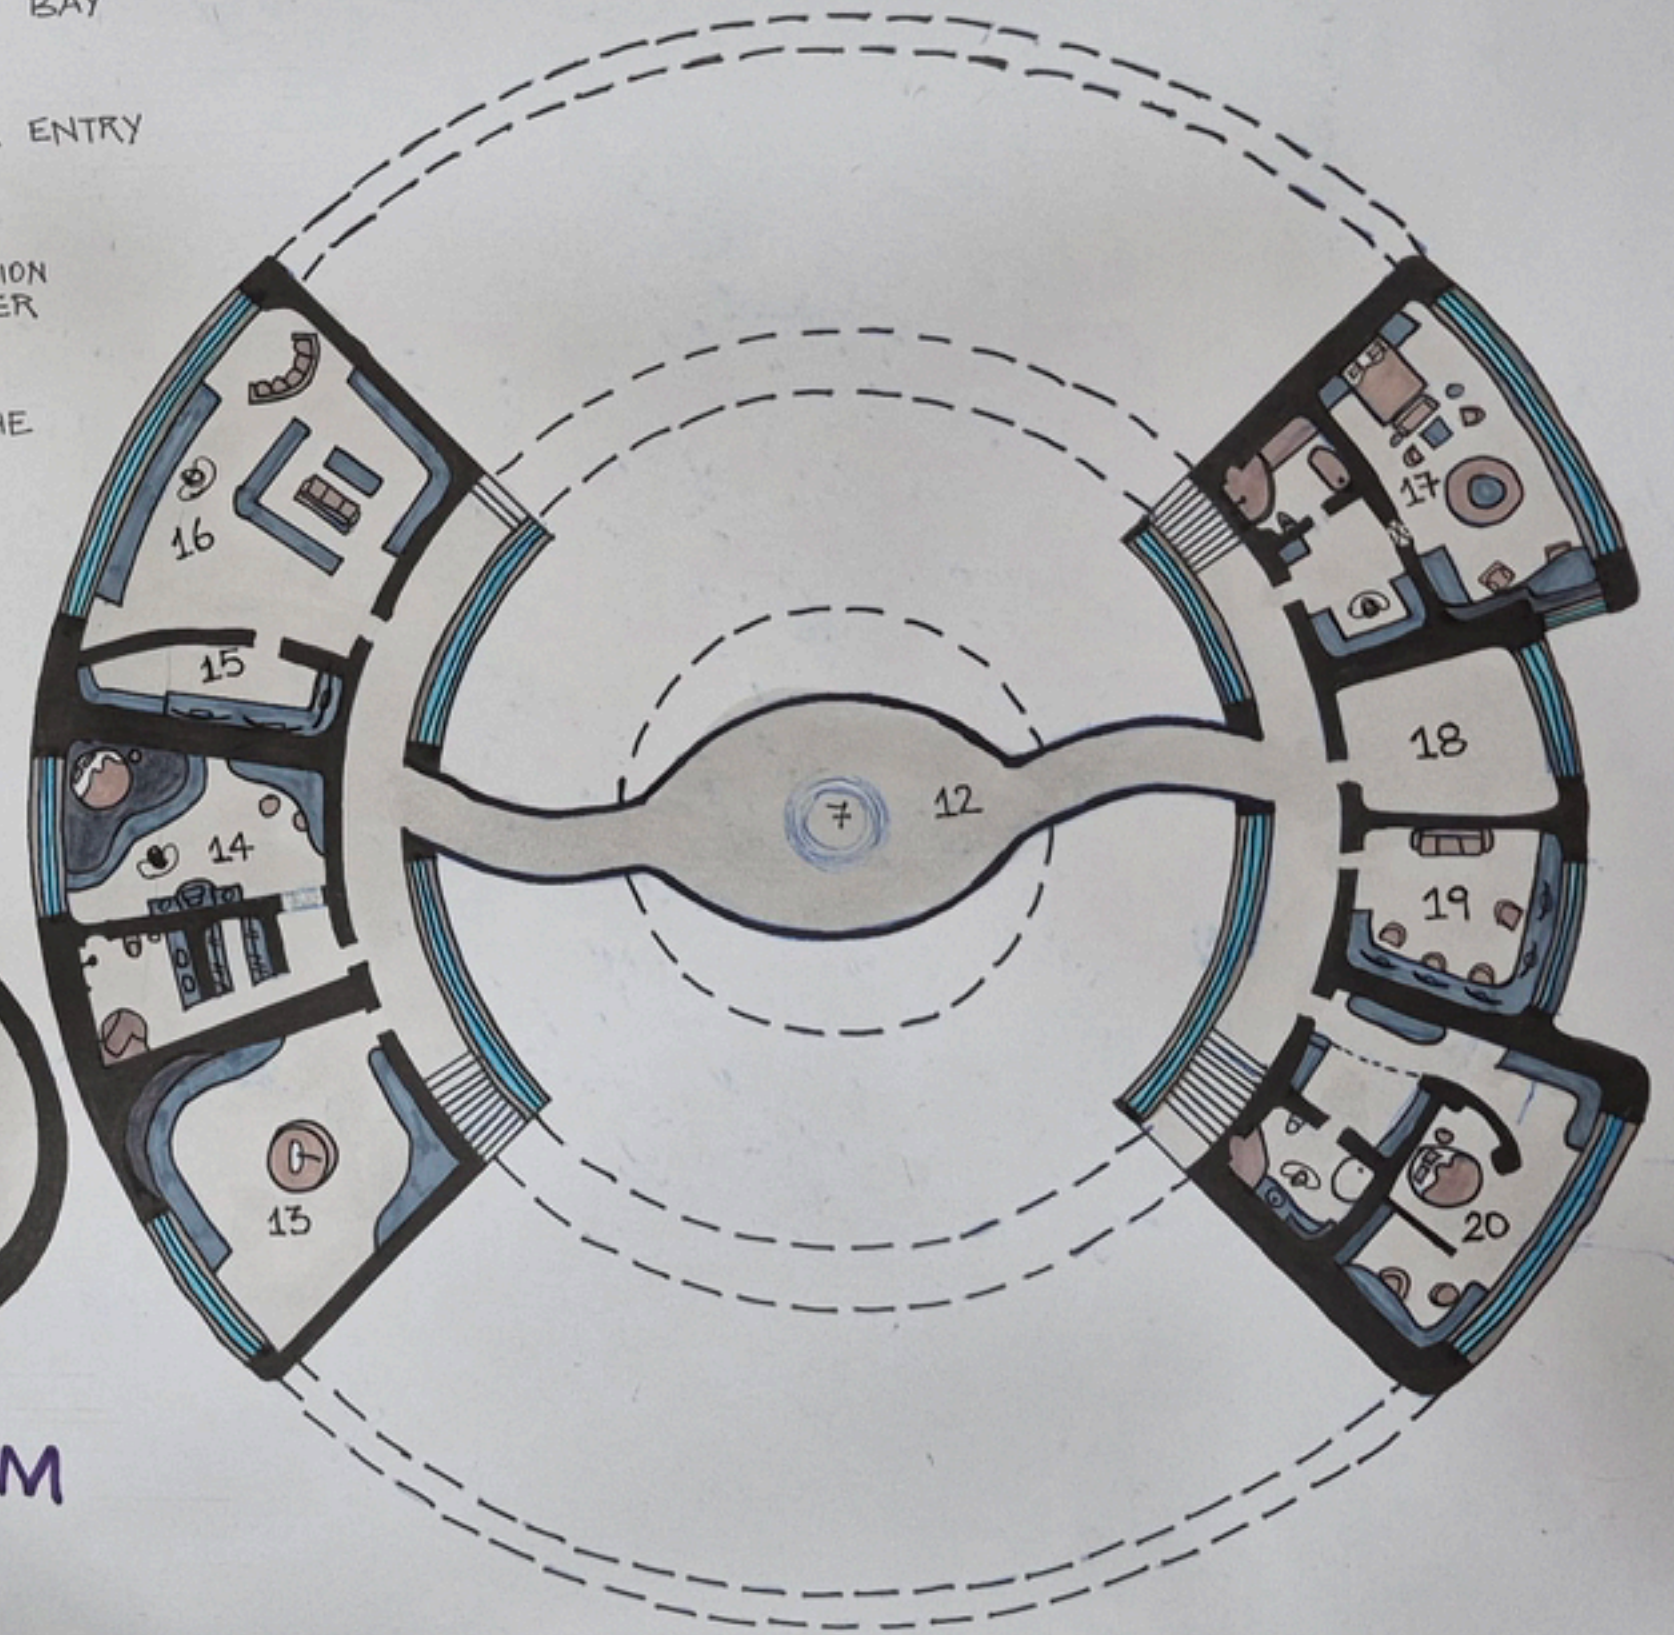

FIRST-FLOOR PLAN