




SITE ANALYSIS

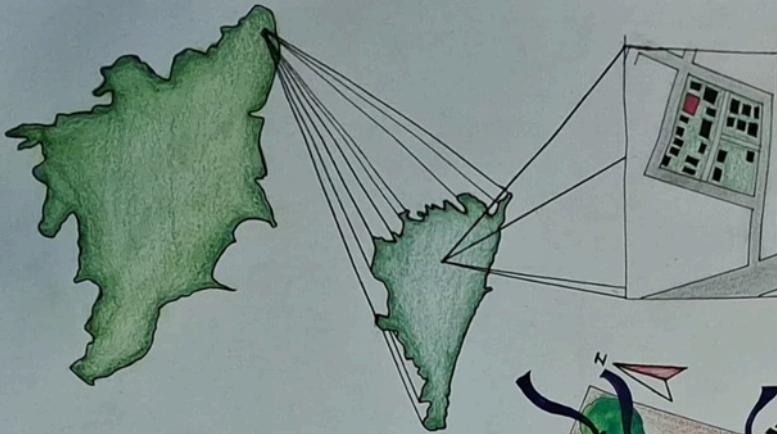

CLIMATE ANALYSIS

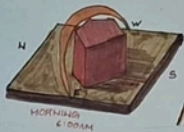

SHADOW ANALYSIS

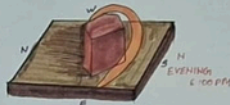

NEIGHBOURHOOD

- PRE-DOMINANTLY RESIDENCE ZONE NEIGHBOURHOOD WITH A CALM AND LOW NOISE ENVIRONMENT.
- PRESENCE OF LOCAL PARKS & OPEN GREEN SPACES ENHANCING LIVABILITY.
- AVAILABILITY OF ESSENTIAL AMINITIES LIKE SCHOOLS, HOSPITALS, ETC.

TYPOLGY


- SURROUNDED BY RESIDENCE LIKE VILLAS AND INDIVIDUAL HOUSES.
- MOSTLY BUILDINGS WITH SHOPS ON GROUND FLOOR & RESIDENTIAL SPACE.

VEGETATION

- RAIN TREE WAS FOUND IN THE SITE PROVIDING A CANOPY.
- FILICE ASHOKA IS ALSO SPOTTED.



- REGIONAL CONNECTIVITY
- GOOD RESIDENTIAL ENVIRONMENT
- MIXED USE DEVELOPMENT

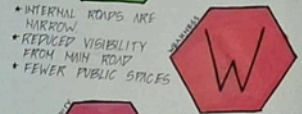

- INTERNAL ROADS ARE NARROW
- REDUCED VISIBILITY FROM MAIN ROAD
- FEWER PUBLIC SPACES



- SCOPE FOR SUSTAINABLE DESIGN
- FUTURE RESIDENTIAL DEVELOPMENT
- RISE OF CONSTRUCTION COST
- FLOODING DURING MONSOON



USER ANALYSIS

BRINDHA SETHU IS AN INDIAN POET, WRITER AND SCREENWRITER.

HER POETRY COLLECTION HAVE BEEN PUBLISHED UNDER THE PEN NAME S.BRINDHA.



NAME BRINDHA SETHU
AGE: 40+
PROFESSION:
AUTHOR, MANAGER,
SCREEN WRITER,
POET.

ADULT DAUGHTER
SISTER-40+
MOTHER-60+
REGULAR GUESTS

MORNING
WAKE UP-5:00AM
COOKING
FIND INSPIRATION

RELAX
5:00PM-6:00PM
TERRACE

NIGHT
LIGHT DINNER
LIGHTS OUT-10:00PM

WORK
7:30AM-4:30PM
MANAGER IN
EDUCATION FIELD

WRITING
6:00PM-9:00PM
ISOLATED


SPACE REQUIRED

AESTHETICS


MOAT
PENTAGONAL PLAN
DORIC COLUMNS
CURTAIN WALLS

VENTILATION

CROSS VENTILATION
NATURAL VENTILATION

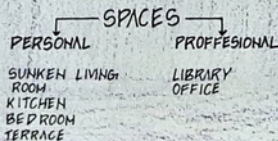


CONCEPT

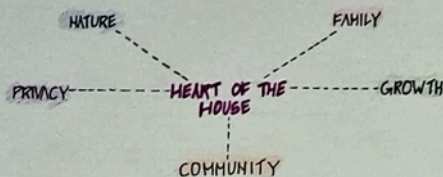

OPEN SPACES
NATURE ORIENTED → WATER




ISLAND COMPONENT - MOAT


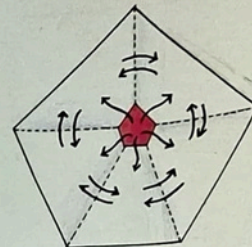


WHY PENTAGON?
SPATIAL CONNECTION
CENTER ORIENTED
EFFICIENT ZONING

FORM DEVELOPMENT

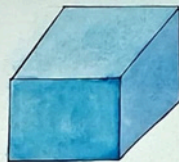

FORM

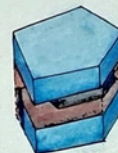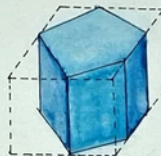




SUBTRACTION





ADDITION

782Msq	FOYER
10.75Msq	SUNKEN LIVING ROOM
11.5Msq	INFORMAL LIVING ROOM
8Msq	KITCHEN
8.25Msq	DINING
14Msq	BACK YARD
12Msq	BED ROOM 1
12Msq	BED ROOM 2
12Msq	BED ROOM 3
6Msq	WASHROOM 1
6Msq	WASHROOM 2
7Msq	WASHROOM 3
10Msq	OFFICE
4Msq	OFFICE WASHROOM
10Msq	LIBRARY
22Msq	BALCONY 1
12Msq	BALCONY 2
15Msq	LOUNGE
25Msq	TERRACE
8Msq	HEAD ROOM
13.16Msq	PARKING

ADJACENT •
 NOT ADJACENT •
 NEARBY •
 NOT RELATED •

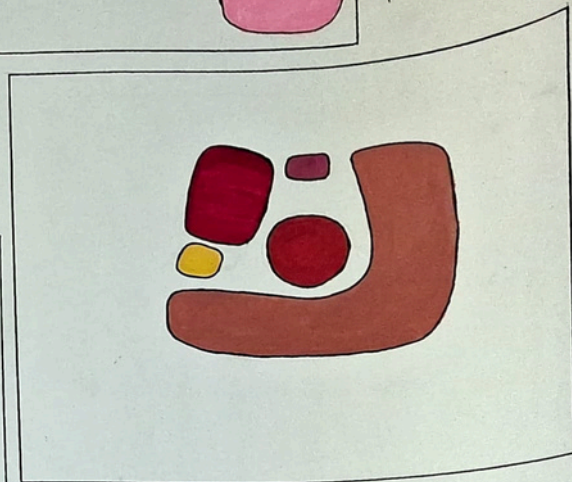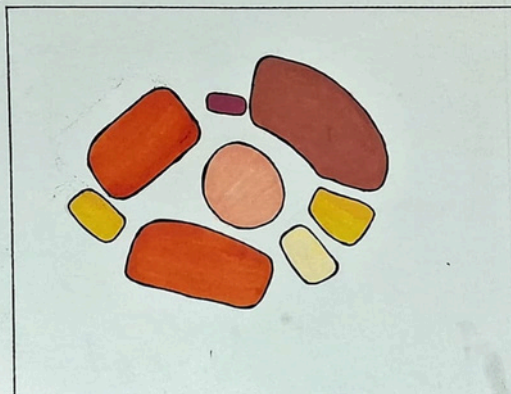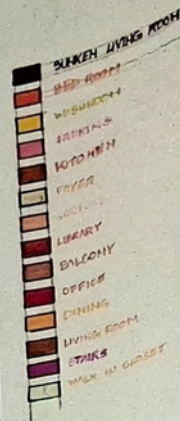

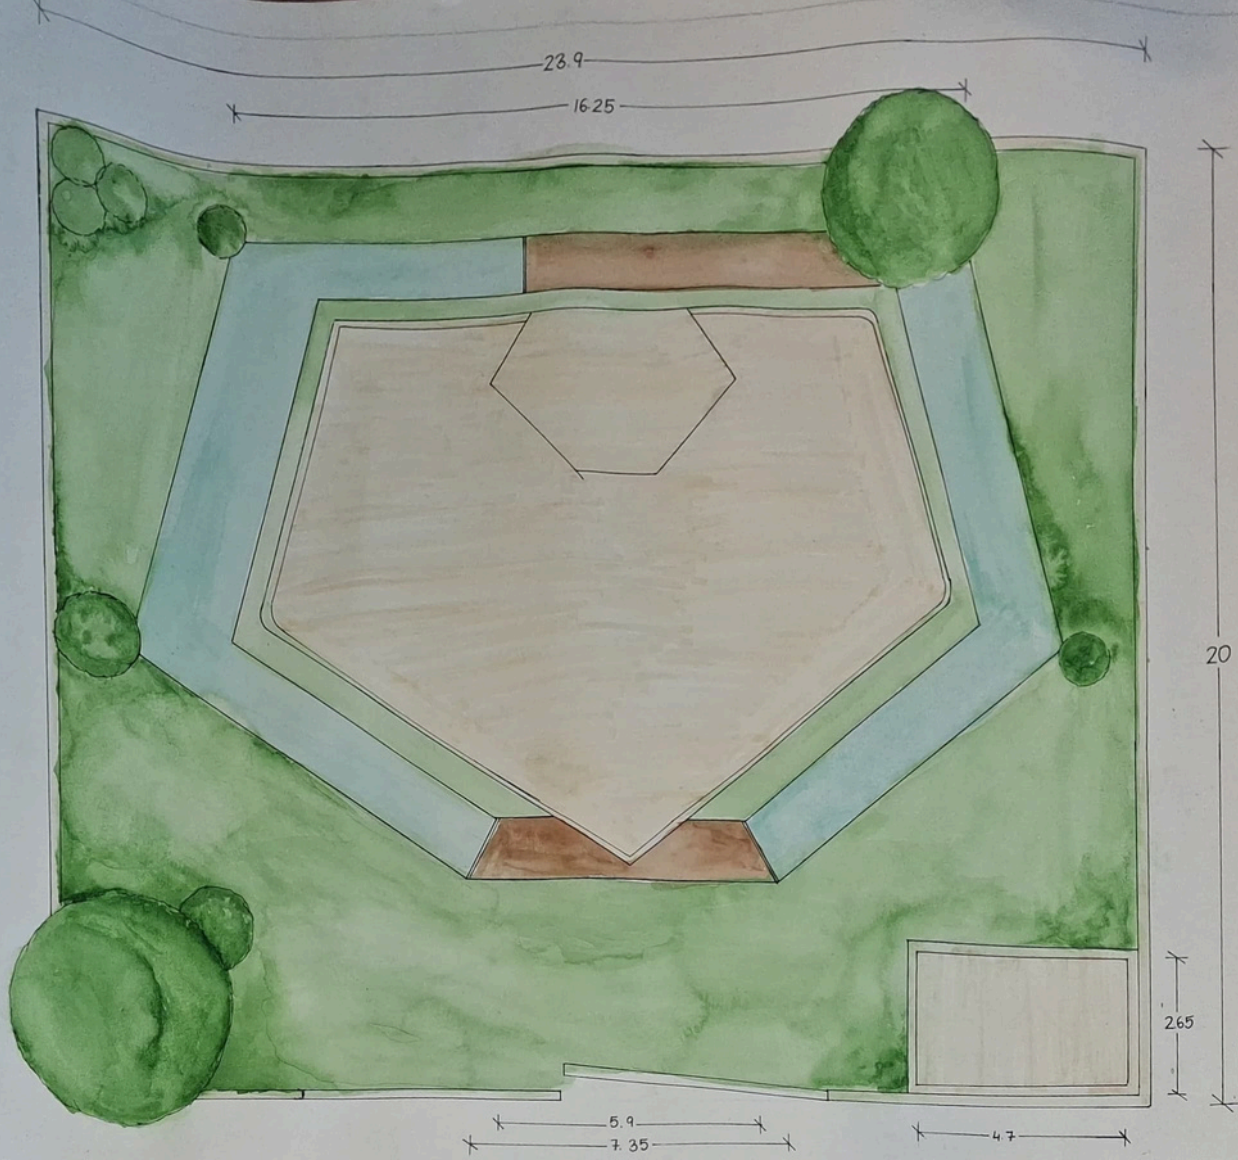


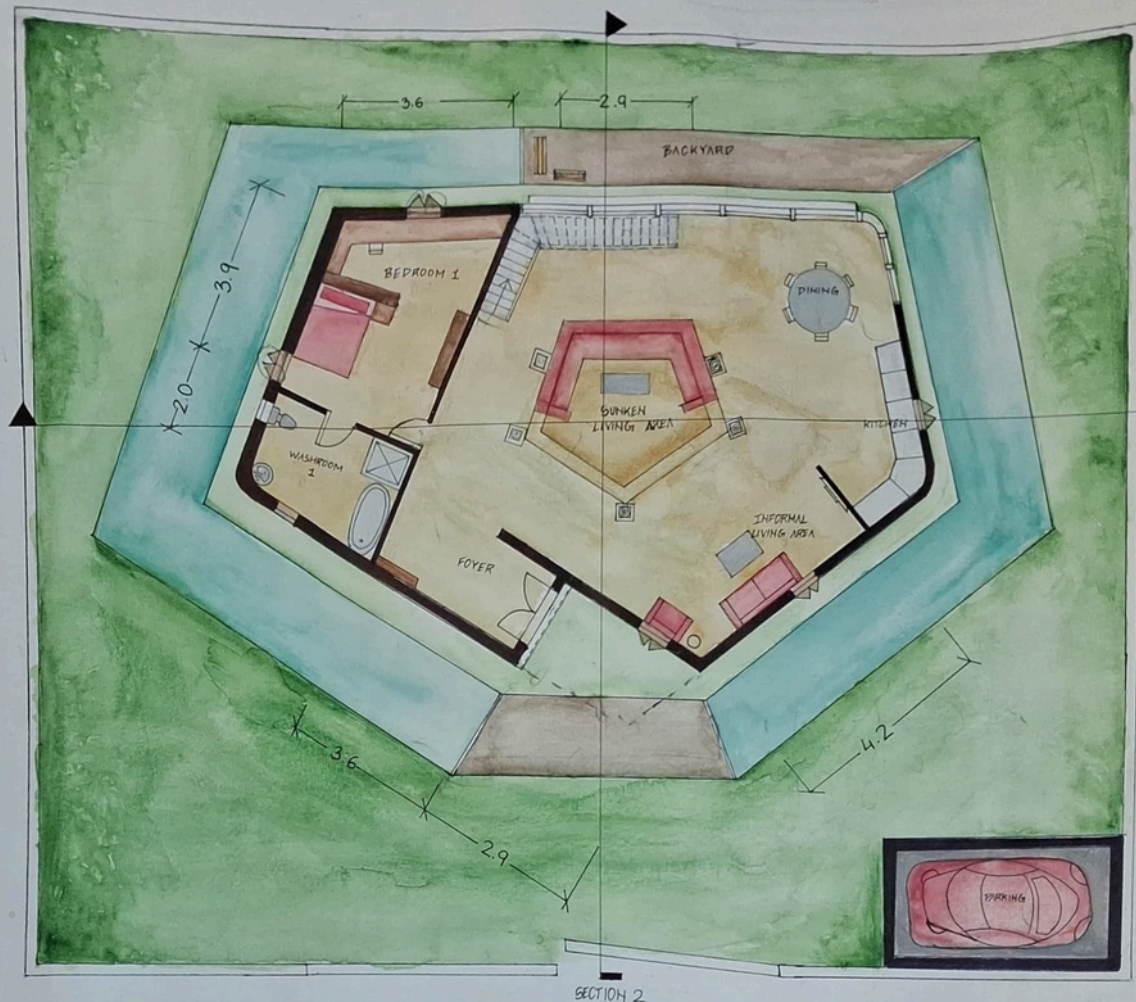

SCALE-1:50

ALL MEASUREMENTS ARE IN
'METERS'


TUH-A-I-IND-0171

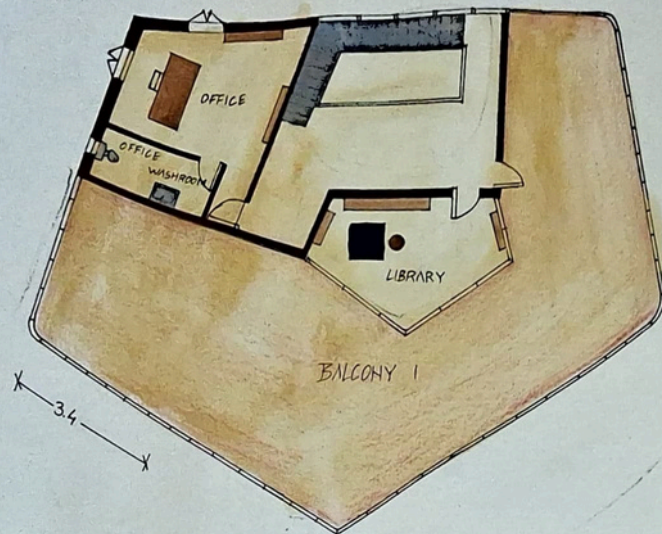


FIRST FLOOR PLAN





SECOND FLOOR PLAN

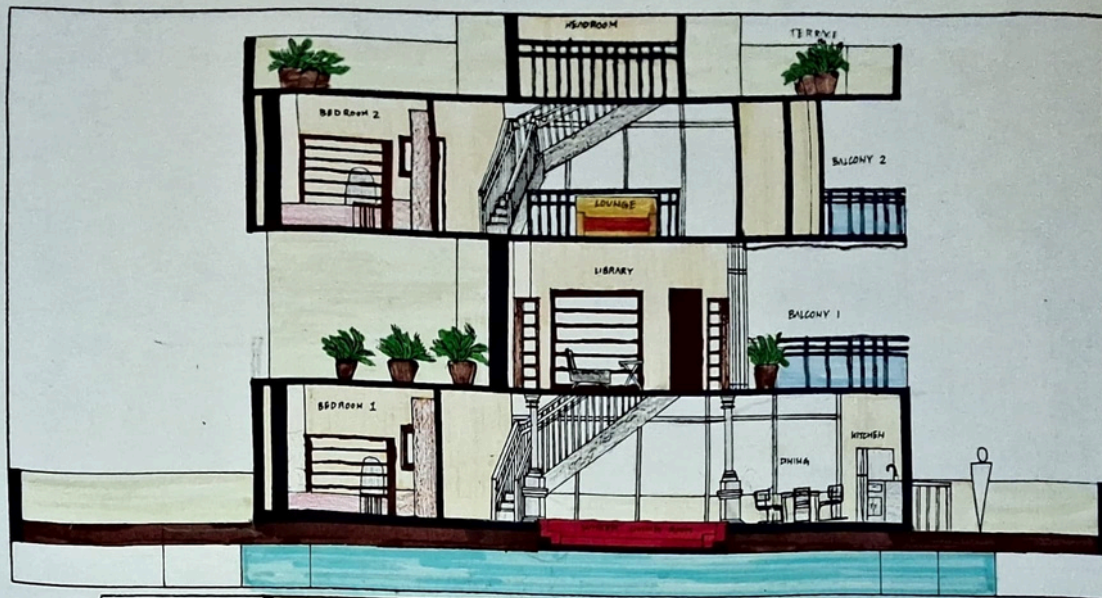

NORTH ELEVATION

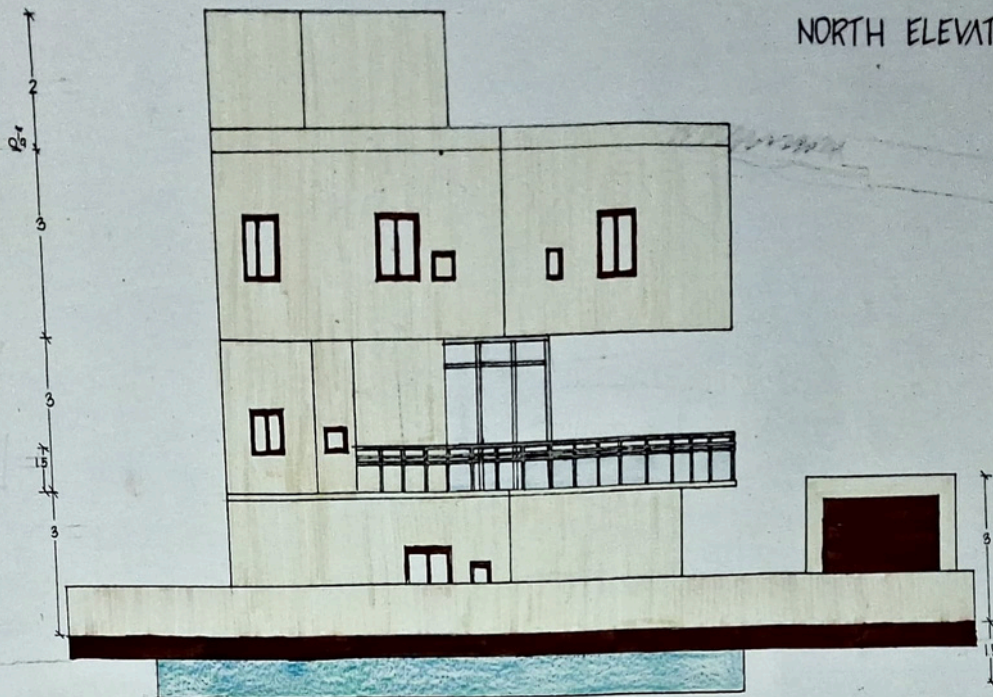


EXTERIOR VIEWS

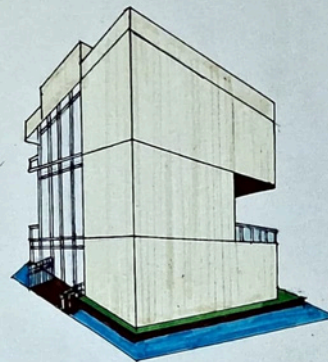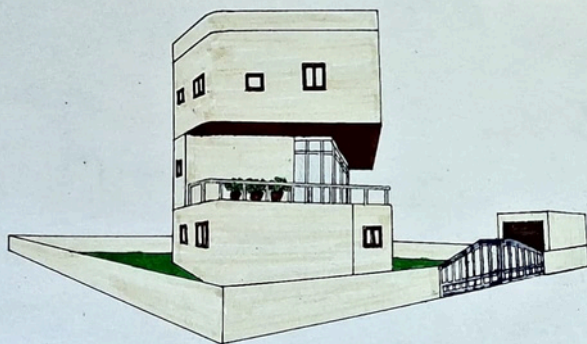



ALL MEASUREMENT ARE
IN 'METERS'

TUH-A-I-IND-0171

EAST ELEVATION

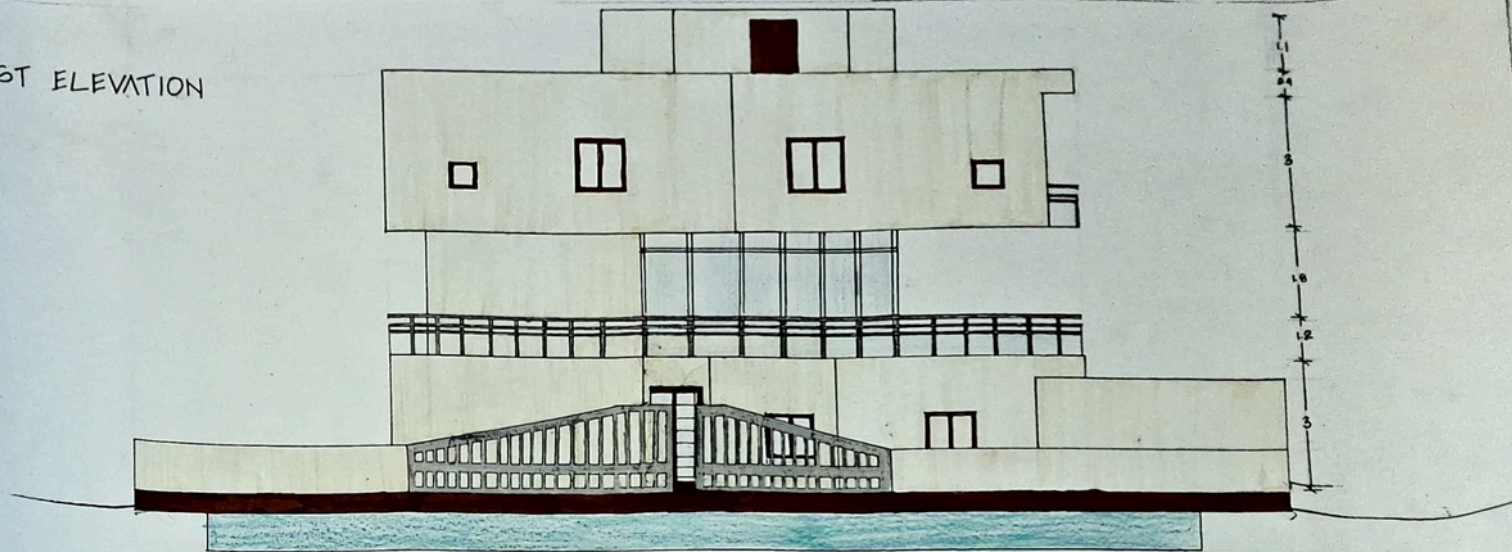

INTERIOR VIEWS

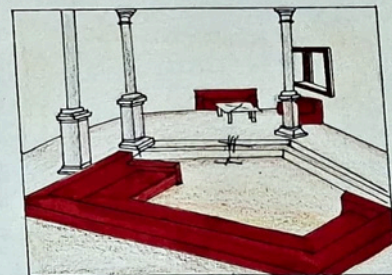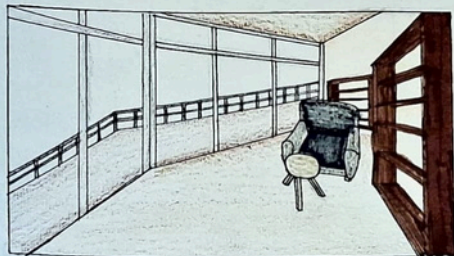

ALL MEASUREMENTS ARE
IN METERS
TUH-A-I-IND-0171