




DR. VANCE : THE SCIENTIST AND DREAMER, FASCINATED WITH THE BLACK HOLE AND WANTING TO STUDY IT FROM CLOSE.




WHAT SEEMED AN OUTLANDISH THOUGHT WAS APPROVED AS AN IDEA THAT WAS REVOLUTIONARY

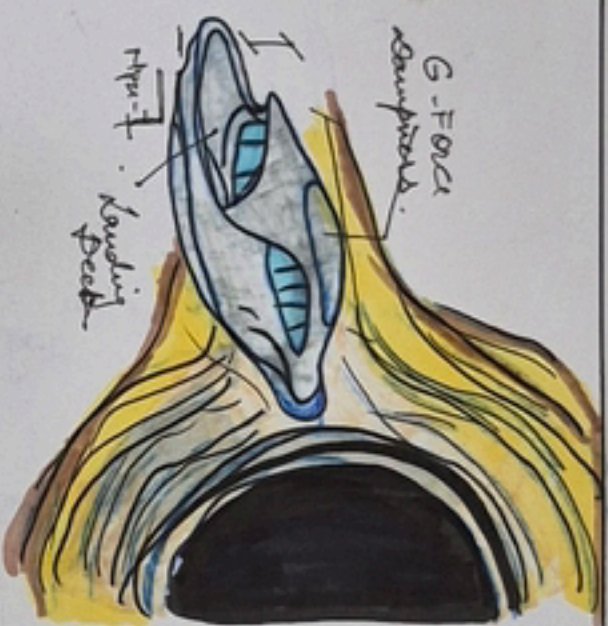

A HOME DESIGNED TO ANCHOR AT THE EDGE OF NYX-7



THE FEROUS JOURNEY: THE READING THROUGH DISTORTED LIGHT.

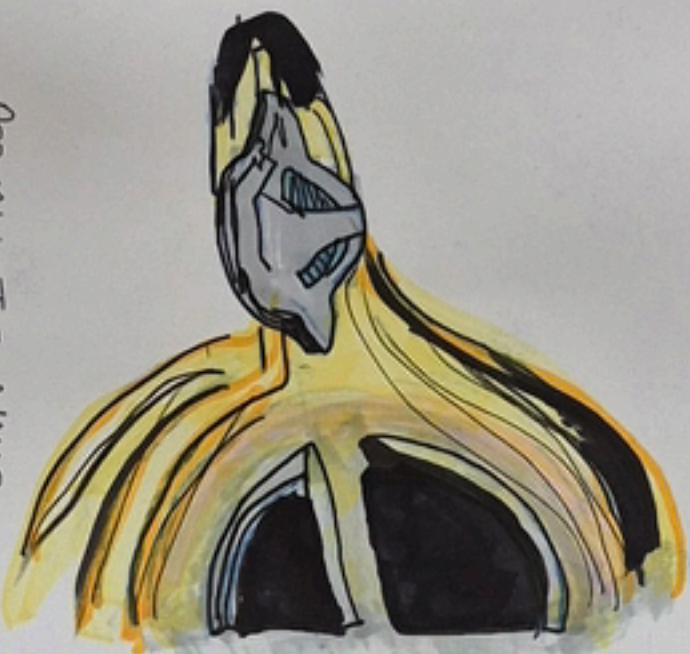

ARRIVAL: THE WALLS WITHSTOOD THE SPACE-TIME PULL

THE VANCE FAMILY REFUSED TO LET HIM GO ALONE, SO THEY DECIDED TO JOIN THIS VENTURE



ARCHITECTURE THAT ORBITS. LIFE THAT ADAPTS.



MR. VANCE SET UP HIS LABORATORY WHILE MRS. VANCE FOUND HER CANVAS.

CONCEPT : THE VANCE HOUSE IS A

HOME SUSPENDED AT THE EDGE OF BLACKHOLE, WHERE TIME SLOWS, GRAVITY BENDS. ORBITING THE EVENT HORIZON OF A BLACK HOLE, IT TRANSFORMS ONE OF THE COSMOS MOST POWERFUL FORCES INTO A PLACE OF SHELTER, DISCOVERY AND BELONGING. DESIGNED FOR A FAMILY OF EXPLORERS, THE HOUSE IS MORE THAN A RESIDENCE - IT IS A SANCTUARY WHERE SCIENCE MEETS EMOTIONS.


SITE CONTEXT : THE SITE IS NOT A PIECE OF LAND BUT A GRAVITATIONAL TERRITORY. THE VANCE HOUSE IS LOCATED IN A STABLE ORBITAL PATH AROUND THE EVENT HORIZON OF A SUPERMASSIVE BLACK HOLE. THE SITE OPERATES AN UNPARALLELED COSMIC VIEWS AND A GRAVITY RELATIONSHIP BETWEEN THE HOUSE ARCHITECTURE AND EQUILIBRIUM. THE INFINITE PULL OF THE EVENT HORIZON MEANINGFUL FOR A HABITABLE, THE HUMAN NEED.

Design Principles :


EMBRACE GRAVITY | TIME & MOTION | SELF-SUSTAINING | CONNECTED TO COSMOS

WATER & VEGETATION : NO NATURAL WATER OR VEGETATION EXISTS. EVERYTHING IS GENERATED AND RECYCLED.


WATER CYCLE

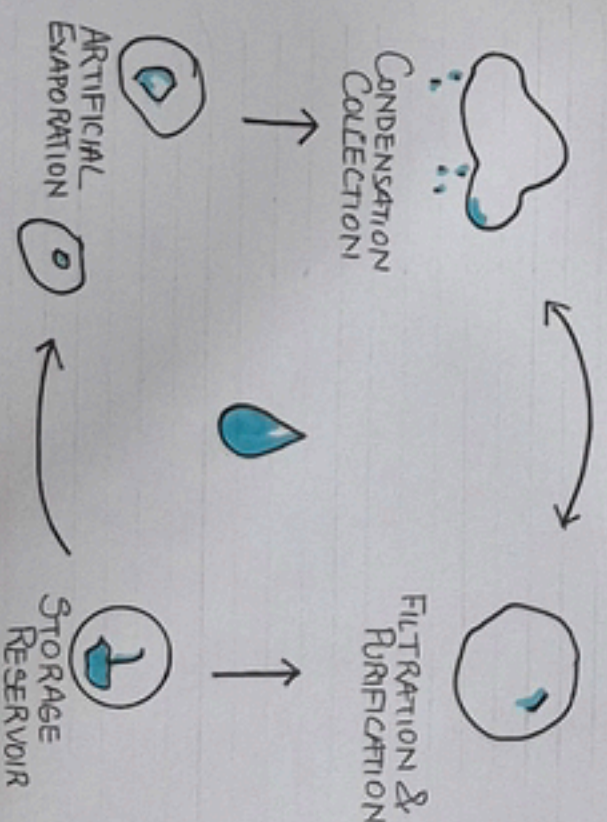


VEGETATION SYSTEM

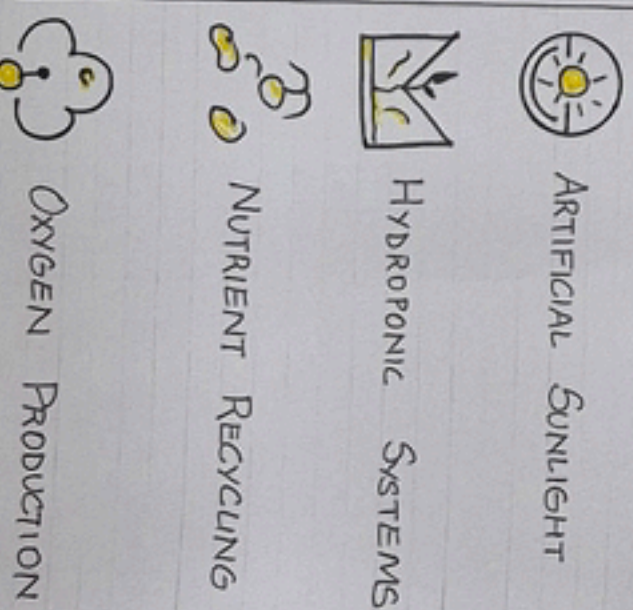


FORM DEVELOPMENT

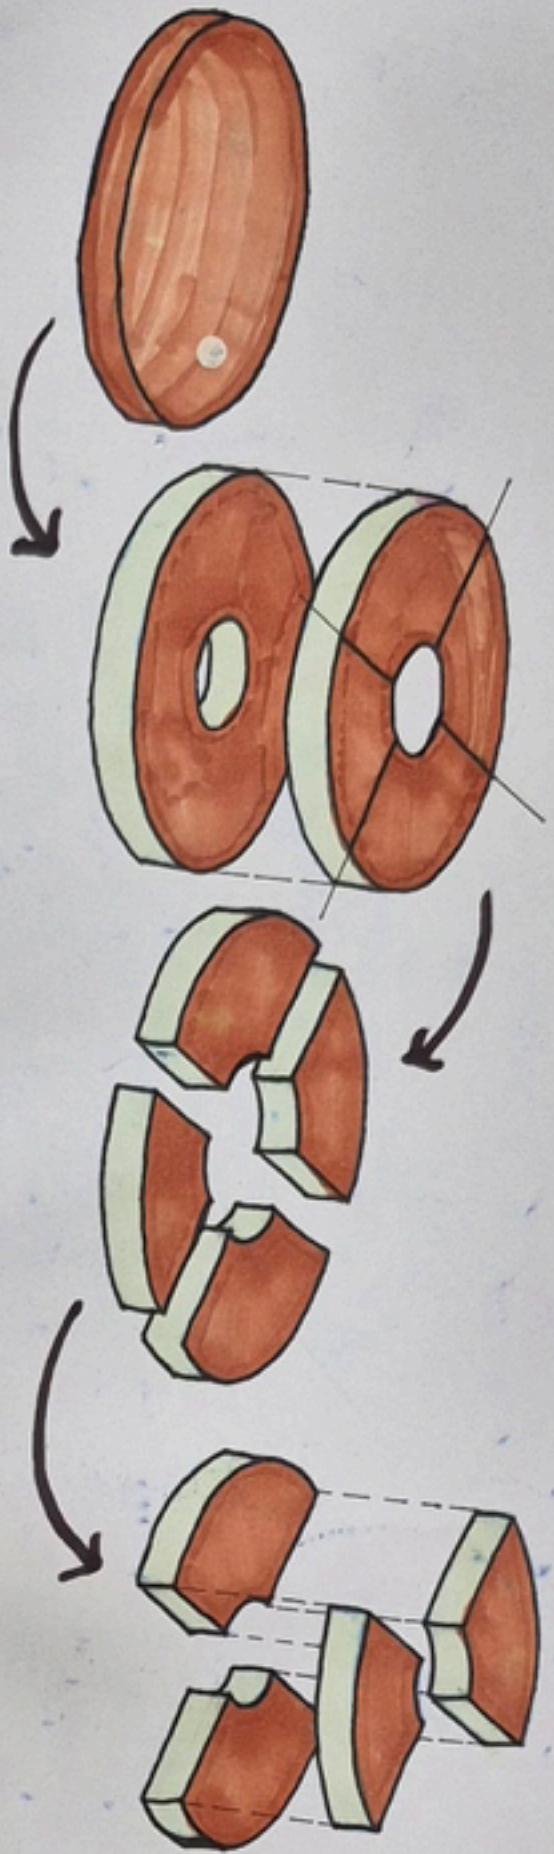

A SOLID CIRCLE TRANSFORMS INTO A RING WITH A CENTRAL VOID, DIVIDED INTO FOUR FUNCTIONAL ZONES AND STAGGERED VERTICALLY TO IMPROVE LIGHT, VENTILATION AND VIEWS.

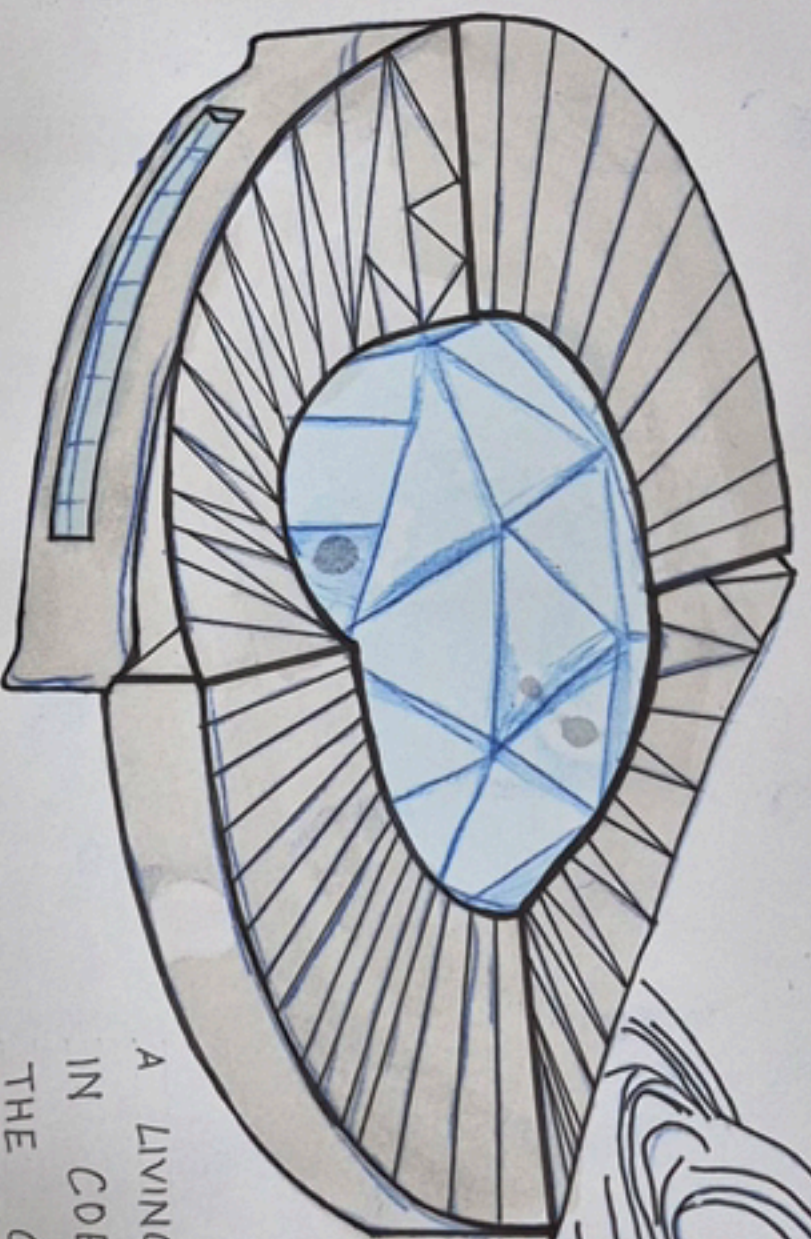


A LIVING EXPERIMENT IN COEXISTING WITH THE COSMOS.

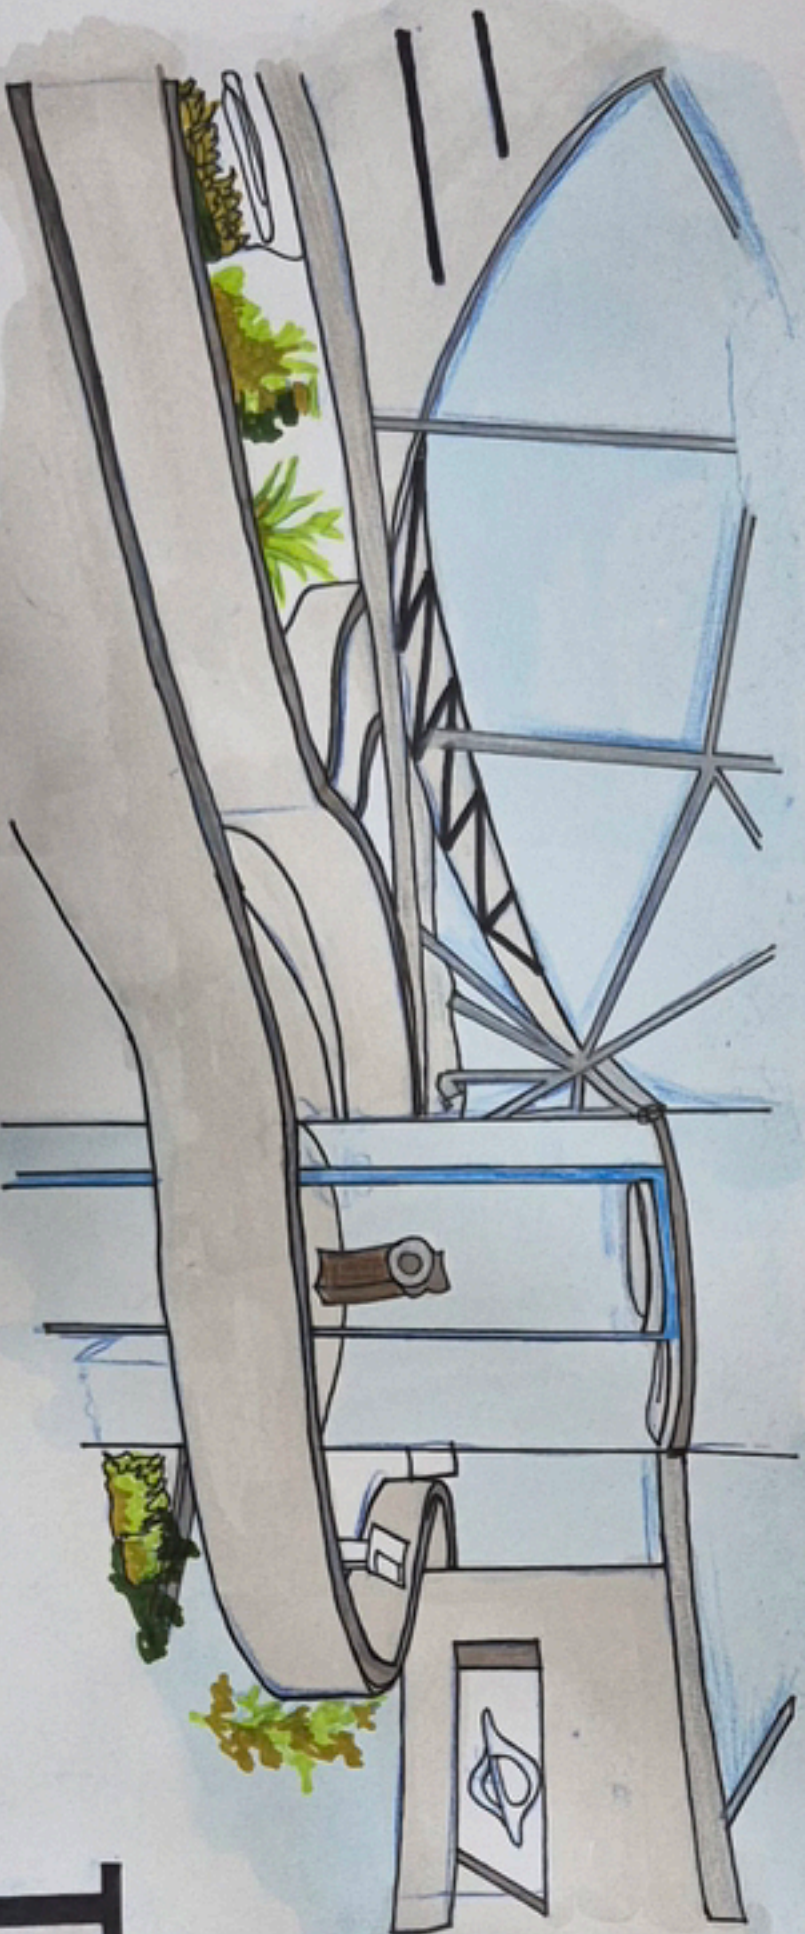


SKYWALK VIEW


THE SKYWALK OFFERS A FUTURISTIC ELEVATED PATHWAY THAT PROVIDES PANORAMIC VIEWS AND A UNIQUE APPROACH TO THE EVENT RESIDENCE.

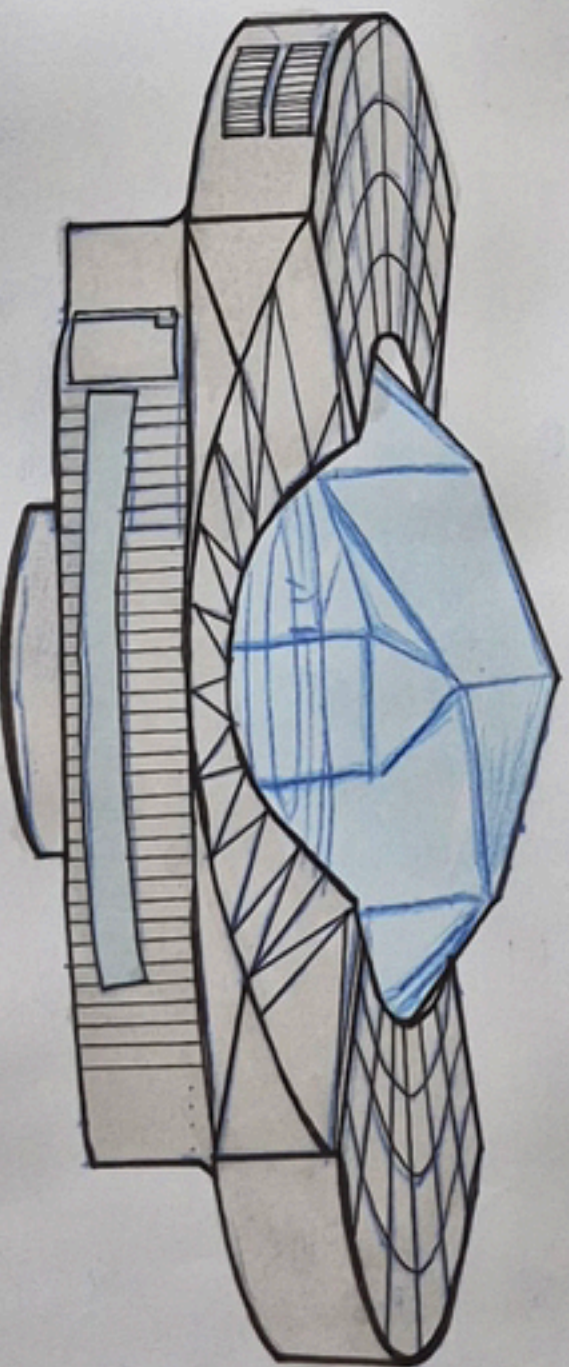

ELEVATION

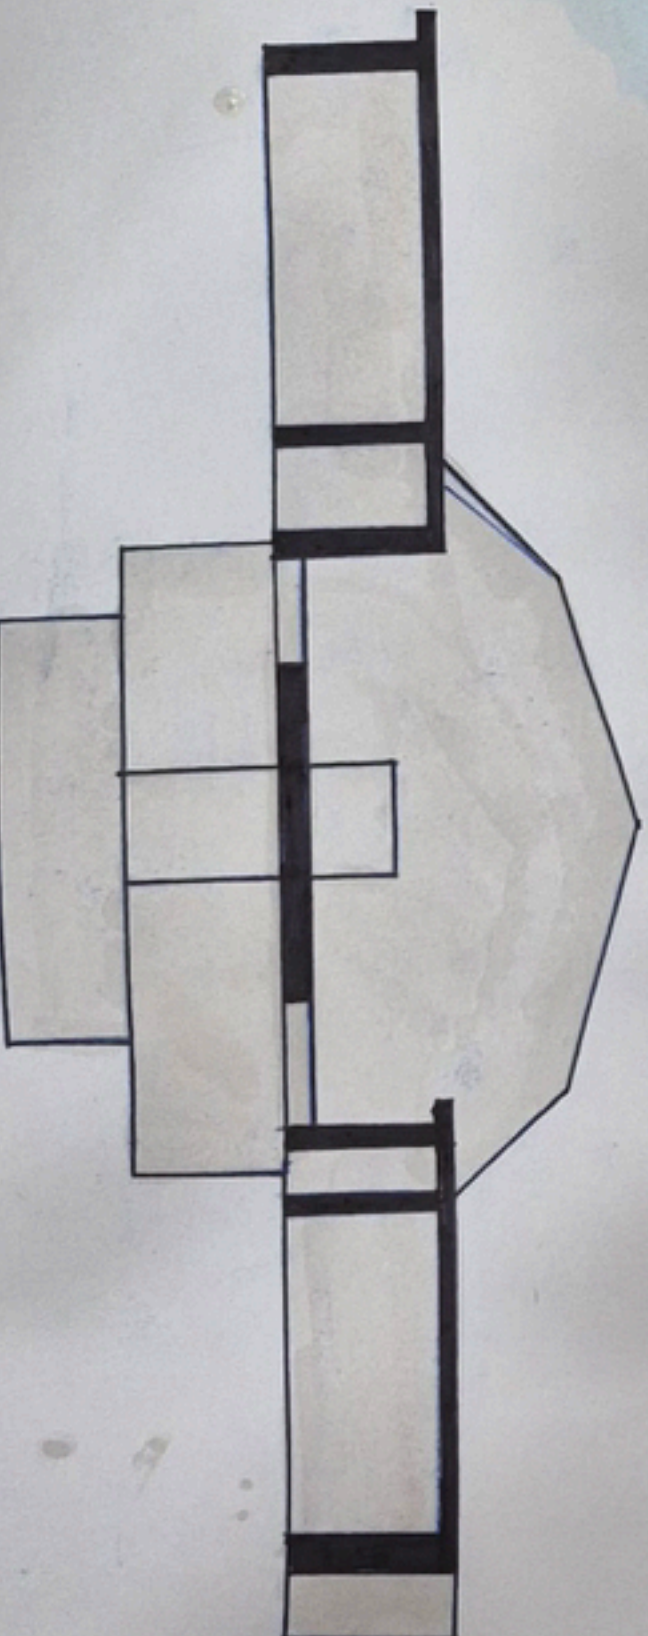

SECTION

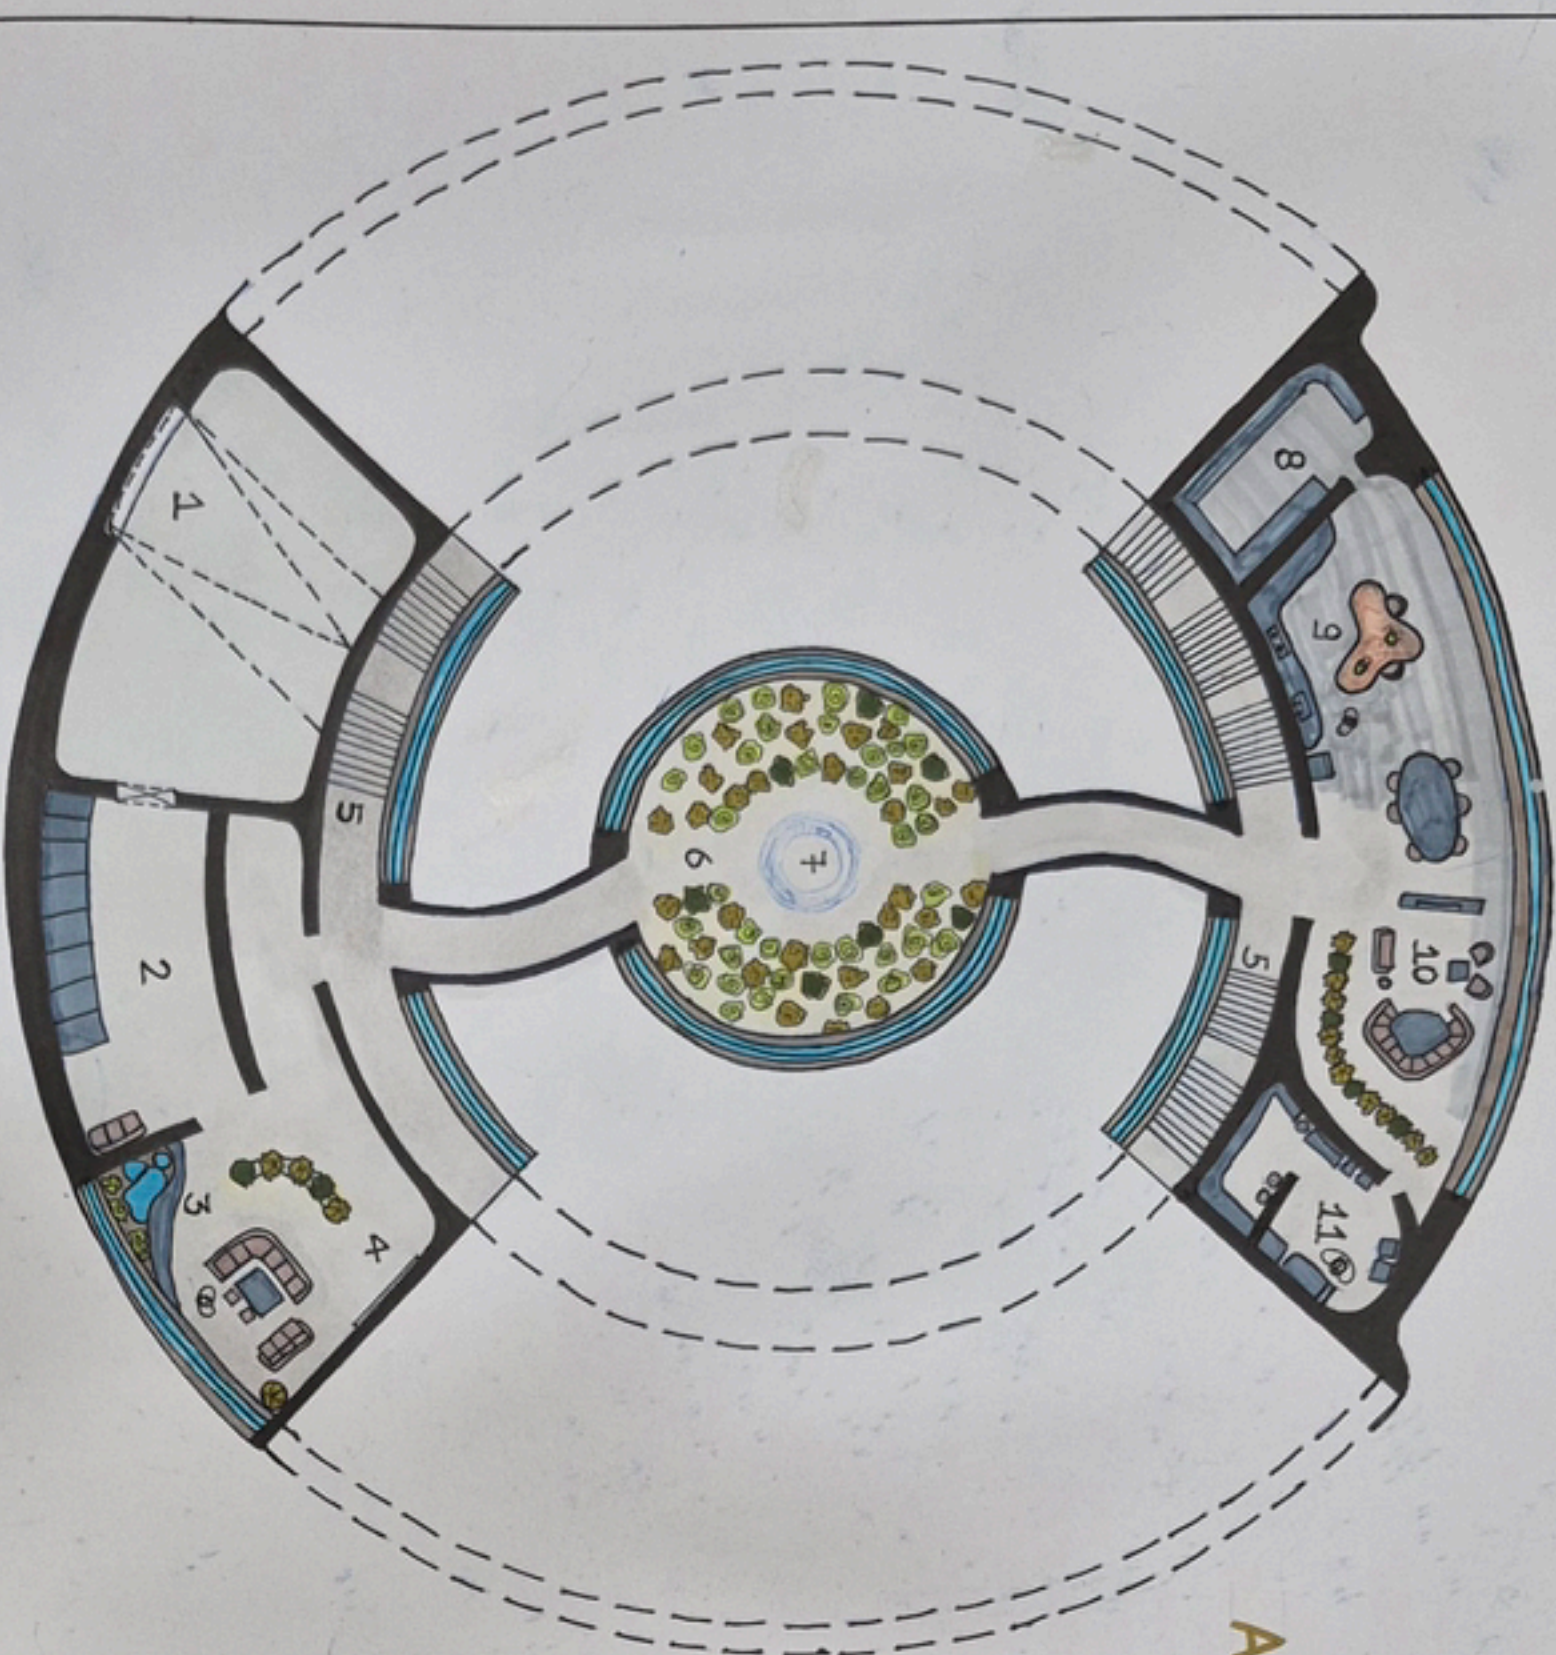

GROUND-FLOOR PLAN

- 1) DOCKING ZONE 12.8m x 8.7m 7) LIFT rad: 1.6m
- 2) SPACE SUIT RACKS 10.2 x 5.58) FOOD STORAGE 3.5m x 6.8m
- 3) INTERIOR POND 9) KITCHEN
- 4) DRAWING ROOM 8.5 x 8.7 10) LIVING ROOM
- 5) STAIRS 11) LAUNDRY/STORAGE 6.8m x 4.2m
- 6) ARBORETUM rad: 6m


Access Sequence

- APPROACH IN SPACECRAFT
- DOCKING AT ARRIVAL BAY
- AIRLOCK ENTRY
- TRANSITION CHAMBER
- INTO THE HOUSE

- 12) SKYWALK 2m wide
- 13) MOTHER'S STUDIO 8.7 x 7.7m
- 14) PARENTS BEDROOM 8.3 x 8.3m
- 15) CONTROL ROOM 8.7 x 2.5m
- 16) MR YANCE STUDY 8.7 x 9.4m
- 17) SON'S BEDROOM 8.6 x 9.3m
- 18) GYM 5.8 x 2.7m
- 19) GAMING ROOM 5.3 x 2.7m
- 20) DAUGHTER'S BEDROOM 8.6 x 9.6m

MAIN WALLS 0.8m THICK
INTERIOR WALLS 0.5m THICK

BASEMENT - MACHINE ROOM

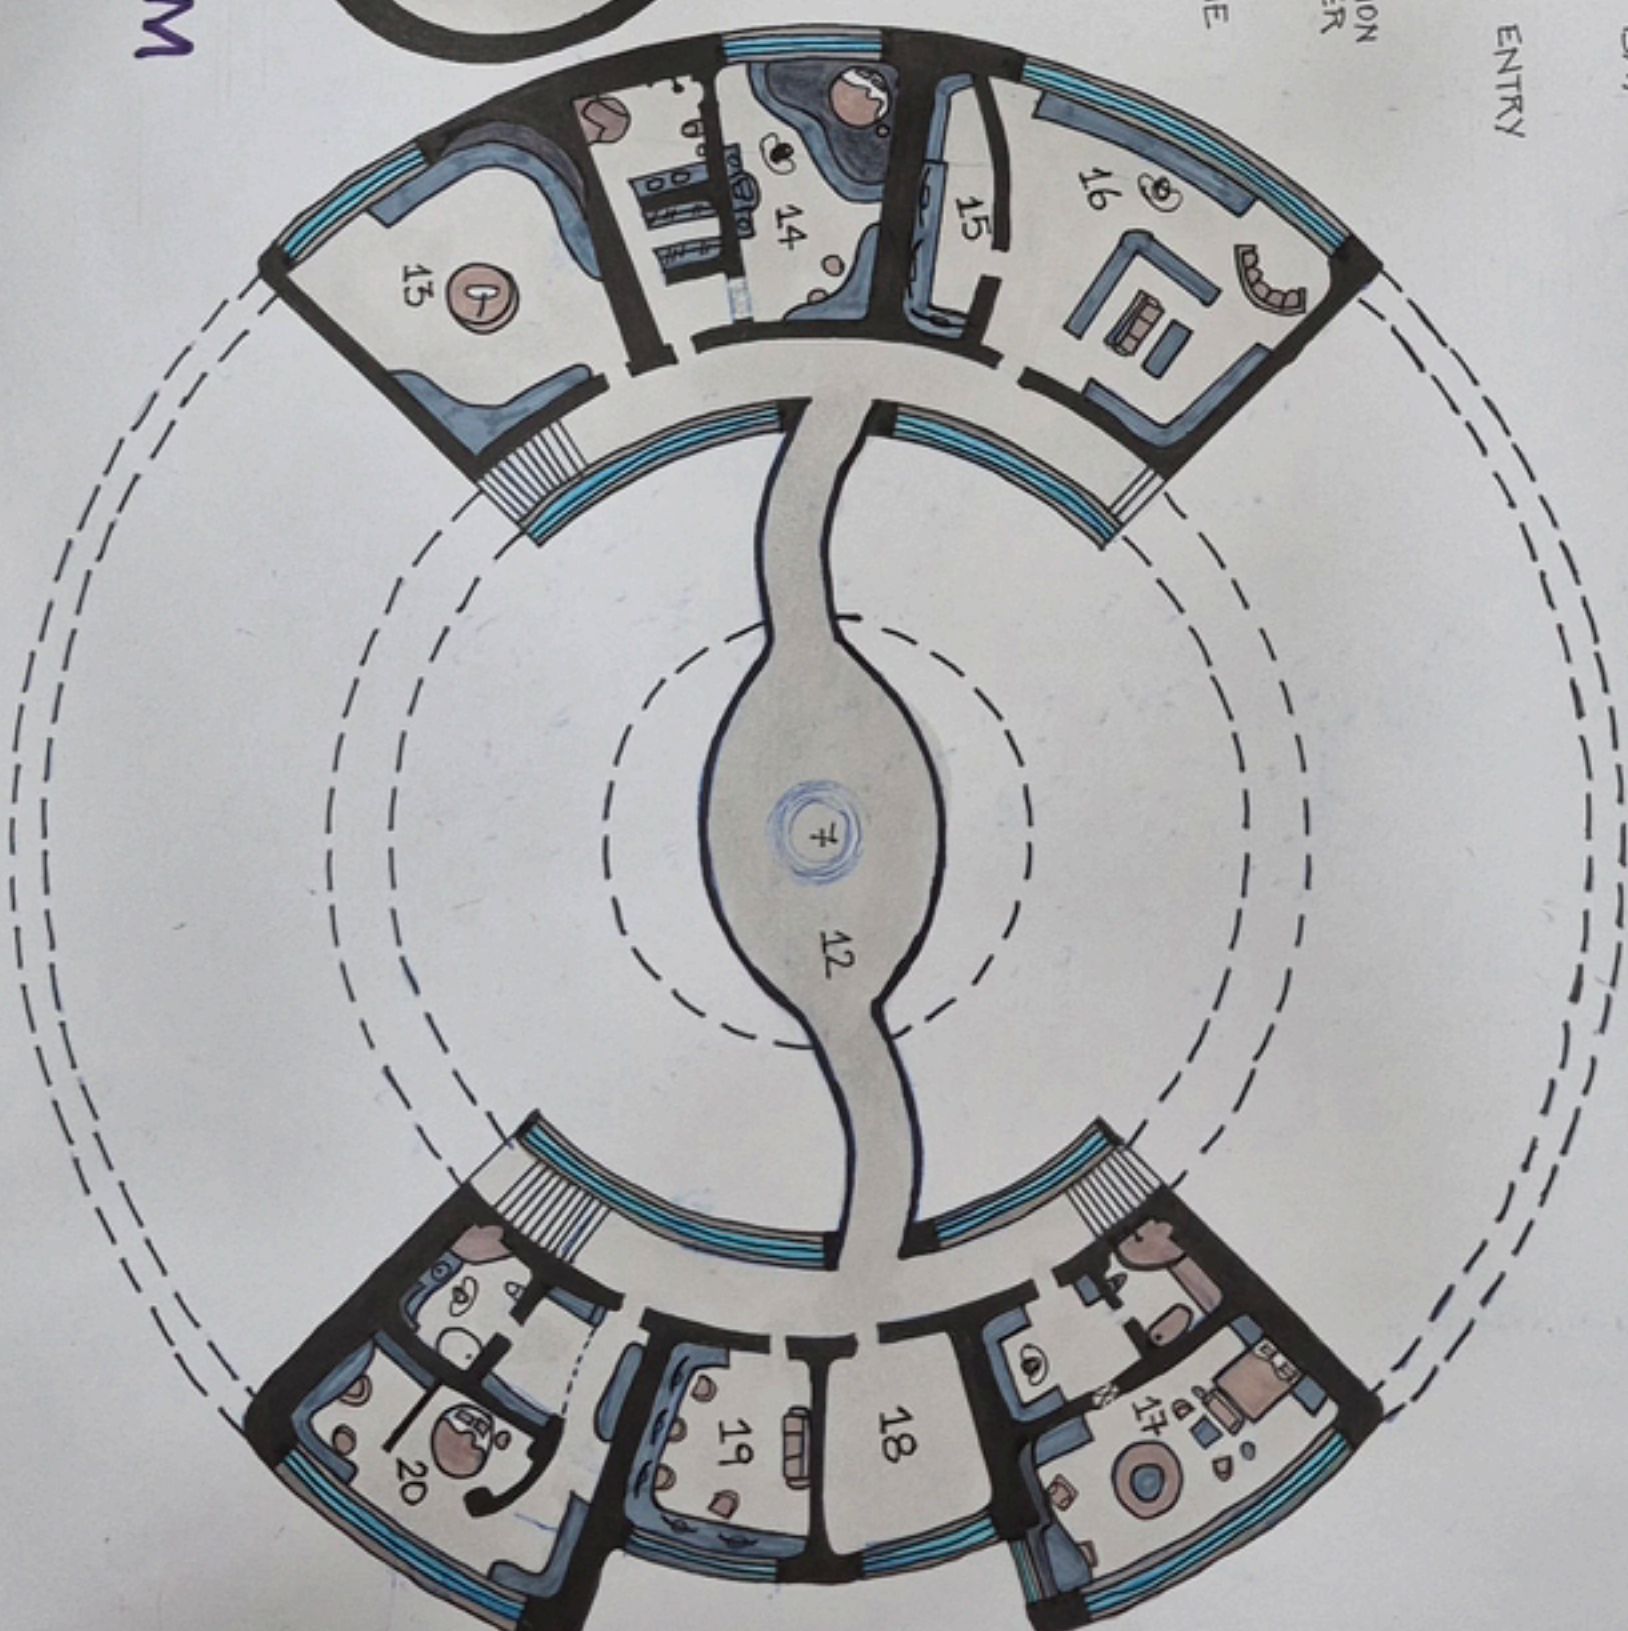

FIRST-FLOOR PLAN