

SITE ANALYSIS

PLANET FIORA

SITE INFORMATION



- GALAXY: LUNORA
- STAR SYSTEM: LUNASIA (Binary)
- PLANET: FIORA
- DAY LENGTH: 29h 32m
- CLIMATE: MODERATE
- SPECIAL PHENOMENON: One hour rainfall every night
- Gravity: $9.81m/s^2$
- ATMOSPHERE: OXYGEN RICH

SITE LEGEND

- SITE BOUNDARY
- BUILDABLE ZONE
- EXISTING TREE (Landmark)
- STREAM
- WIND DIRECTION

DUAL SOLAR PATH


Two Stars movement across sky

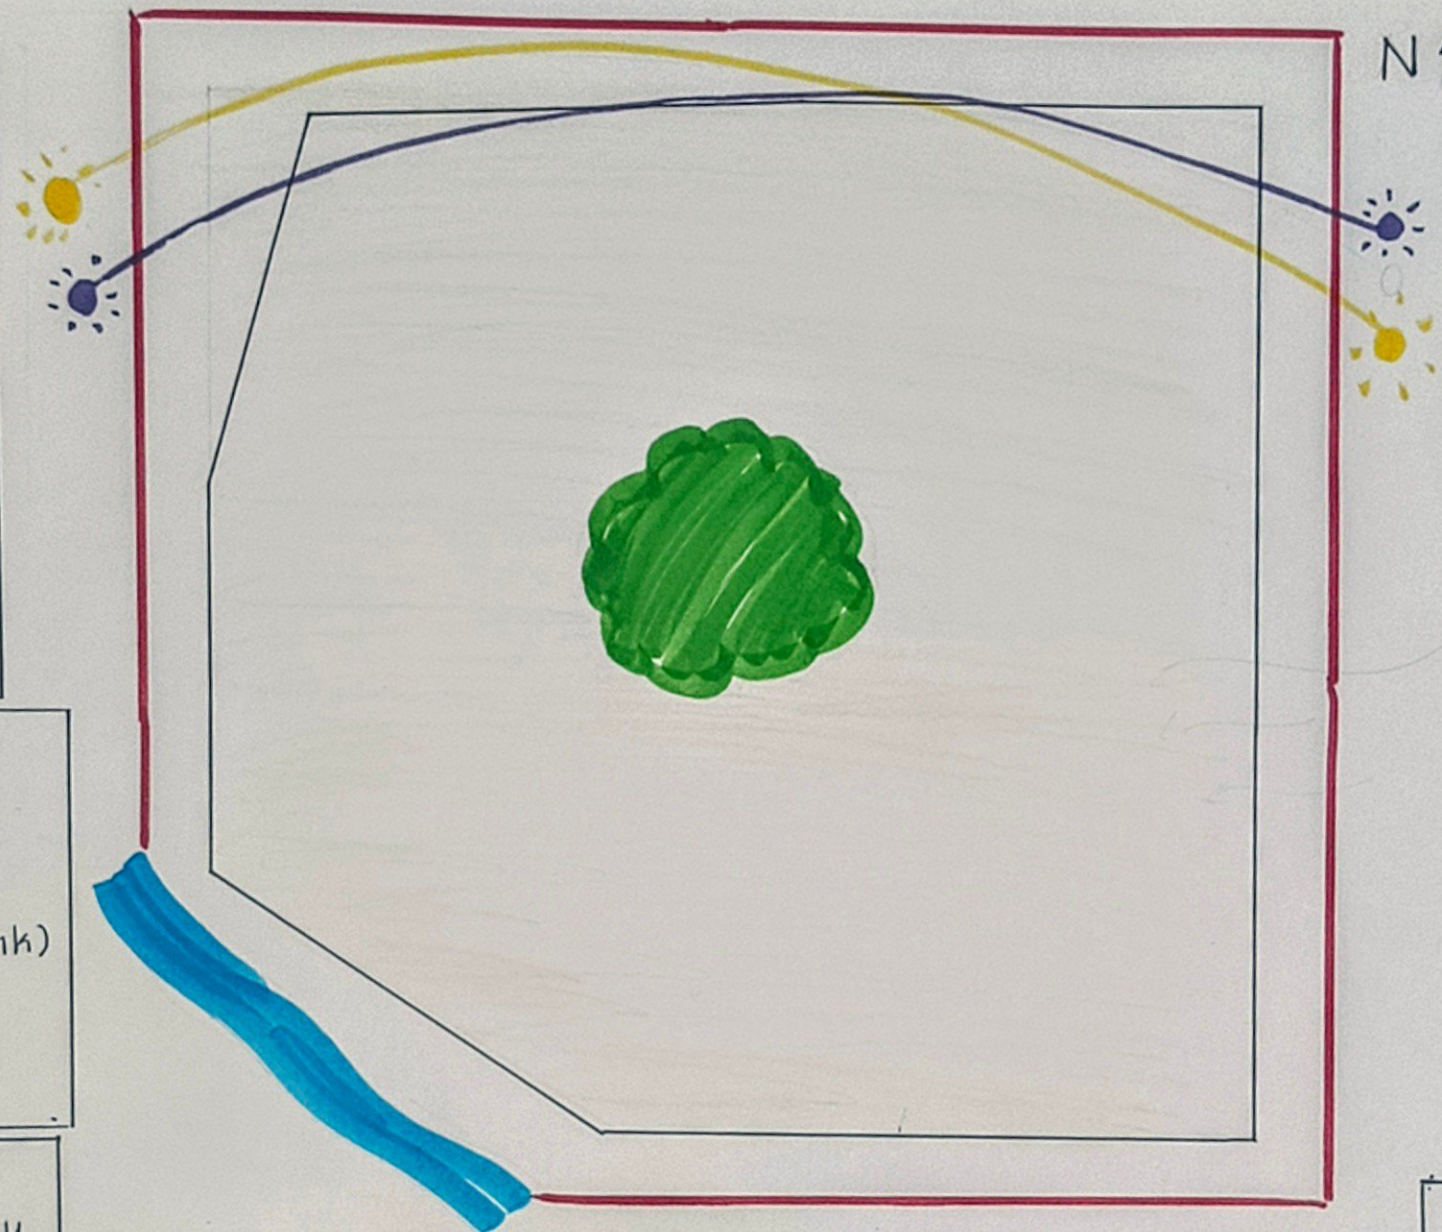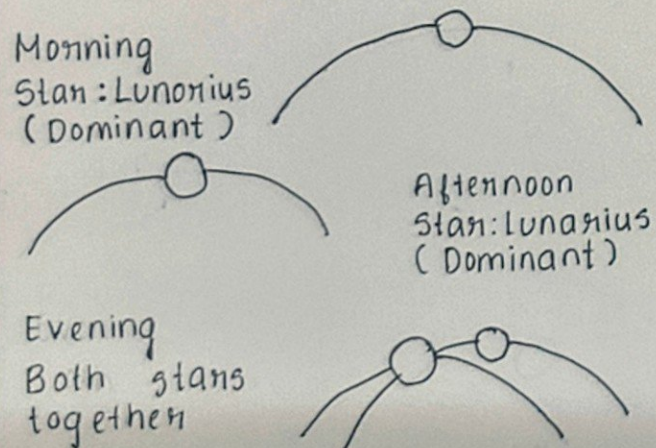

VIEWS FROM SITE

- ① → Twin star sunrise
- ② → Mountain range
- ③ → Stream
- ④ → Open grassland
- ⑤ → Evening sky

NIGHT RAINFALL

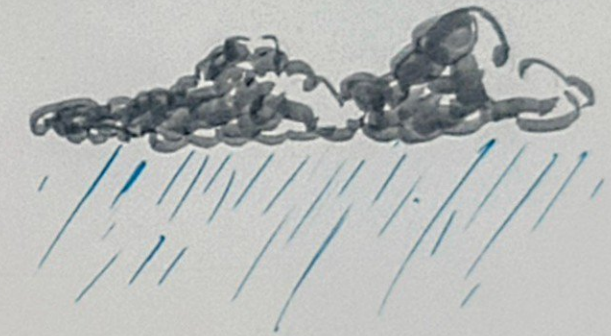


One Hour every Night

SOIL PROFILE



Top soil (Fertile)
Mineral sand
Weathered rock layer
Structural Stone

NATIVE VEGETATION

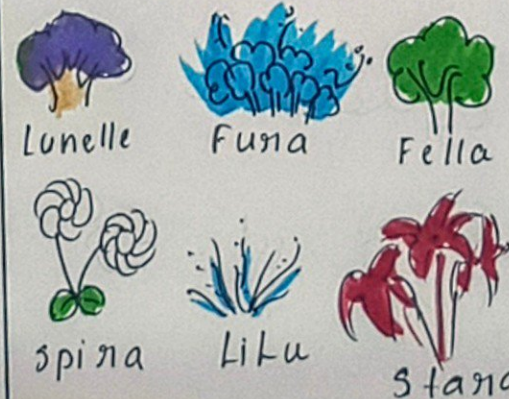

SITE OPPORTUNITIES

- Existing tree
- Stream
- Pleasant climate
- Rich native vegetation
- Night rainfall for water harvesting

SITE CONSTRAINTS

- Preserve tree
- Do not disturb stream
- Protect native vegetation
- Minimize ground disturbance

THE VANCE FAMILY

USER ANALYSIS



MR. VANCE
(Father)

- Nature observer
- Reads and studies
- Maintains water collection system



MRS. VANCE
(Mother)

- Loves gardening
- Enjoys cooking
- Loves family time (gatherings)

CYAN WATER

- Fine soil mixes to form many construction materials with it
- Naturally pastel cyan colour.
- Collected through rain harvest
- Rich in minerals

SPECIAL SOIL (SAND)

- Fine mineral rich soil
- Reacts with cyan water
- Naturally abundant.
- Sustainable and renewable source.
- Forms different materials.

STONES (TYPES)

- Hard stone: for walls, foundation
- Soft stone: flexible, shock-absorbing (for chairs, sofas)
- Blends seamlessly with landscape.

(They never cut trees as their soil and water can form plenty of materials)

SPATIAL NEEDS



Garden and Outdoor Seating

Quiet study corner for reading and focused work



Rainwater count experience nightly rainfall and illuminated channels

View towards the stream peaceful visual connection with the landscape




LILLIA VANCE
(Daughter)

- Loves drawing
- Plays around Lunelle tree
- Watches illuminated water channels at night.



ETHAN VANCE
(Son)

- Curious explorer
- Collects interesting stones and crystals
- Observes twin stars.

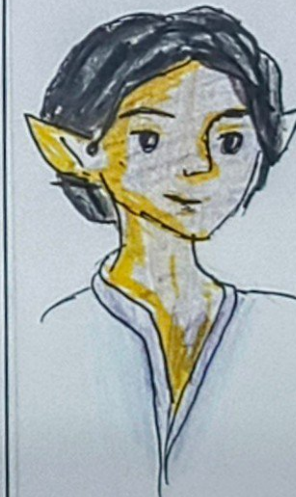


CONCEPT EVOLUTION



VEGETATION




MATERIALS

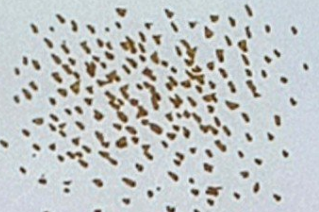


• Soil, when mixed up with cyan water gives different construction materials.

• Water on the planet is of pastel cyan colour naturally

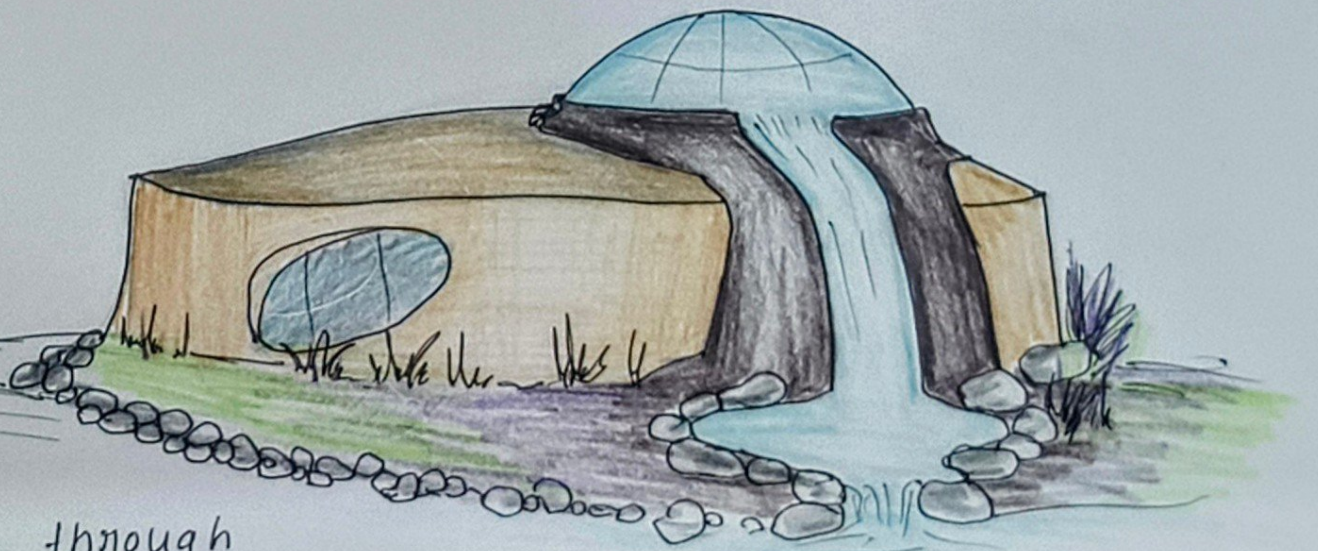

Night rain time is like a daily ritual. They worship rain by sitting together with family (builds good relationship among members). Over the living room, a transparent dome is present which illuminates when cyan water pours. It flows to the garden pond, then to the stream through water channels.

PLAN

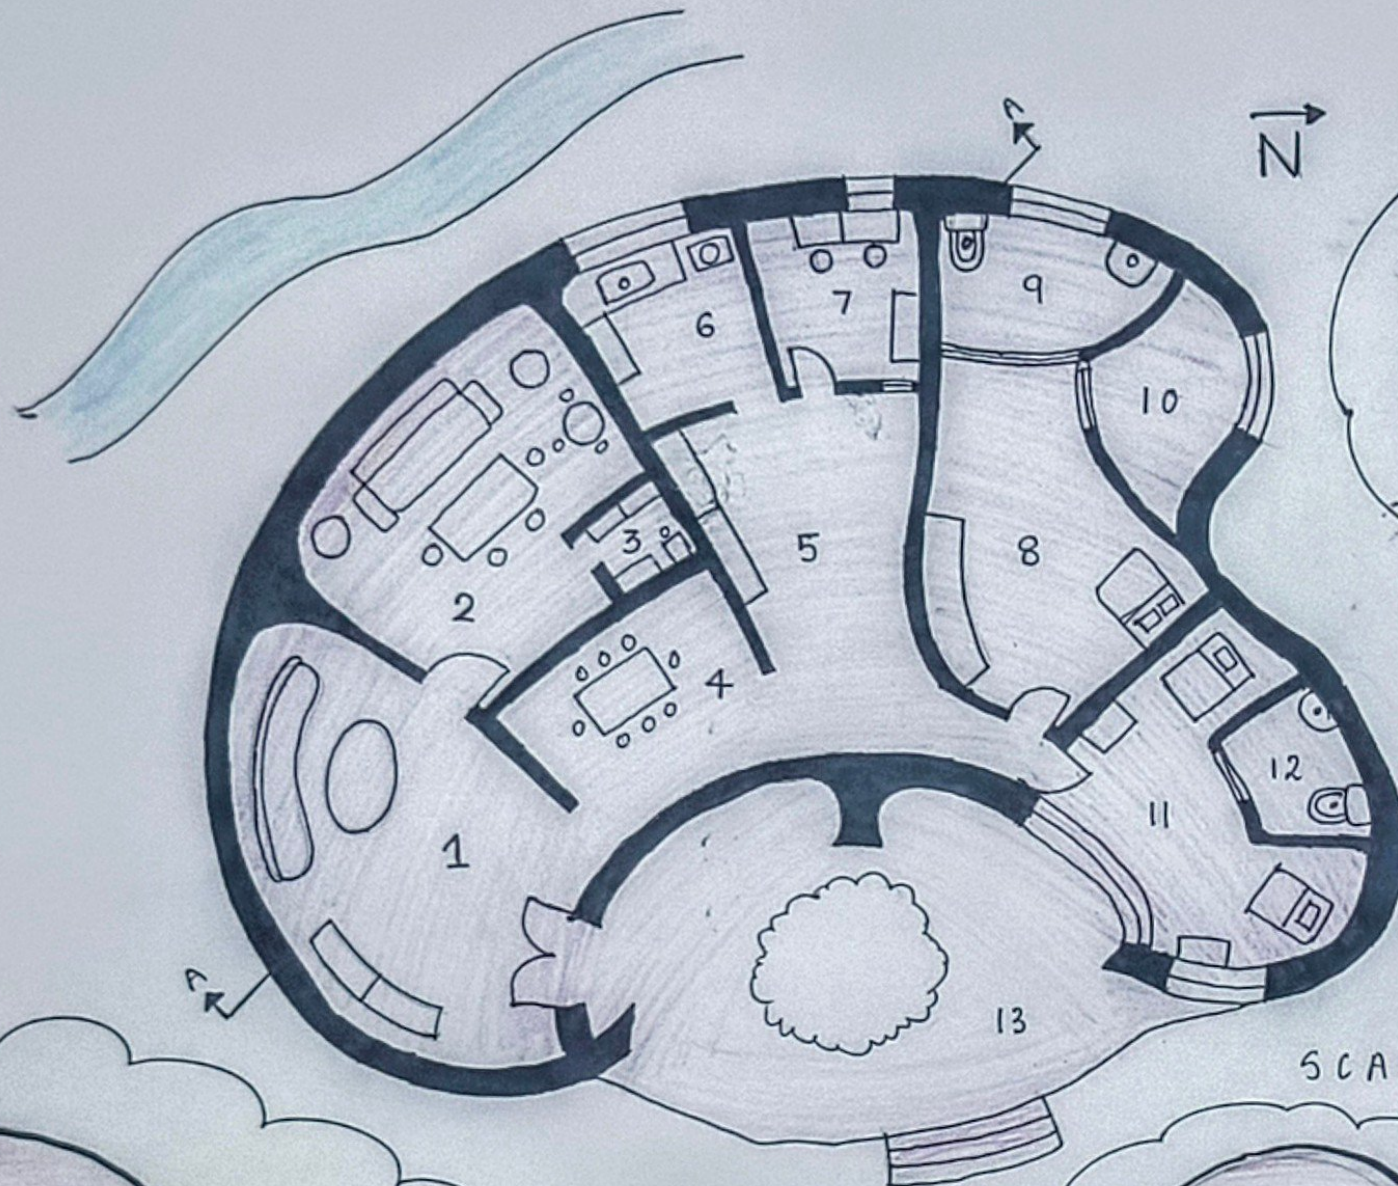

SCALE: 1:100




SECTION - A-A

AIM


- A home that flows with land
- Space arranged around nature
- Curved wall for harmony
- Rainwater harvested from roof to stream

LEGEND

1. Living room
2. Drawing room
3. Reading corner
4. Dining room
5. Kitchen
6. Work area
7. Study room
8. Bedroom (I)
9. Bath + Toilet (I)
10. Storage (cloths)
11. Bedroom (II)
12. Bath + Toilet (II)
13. Vanandah

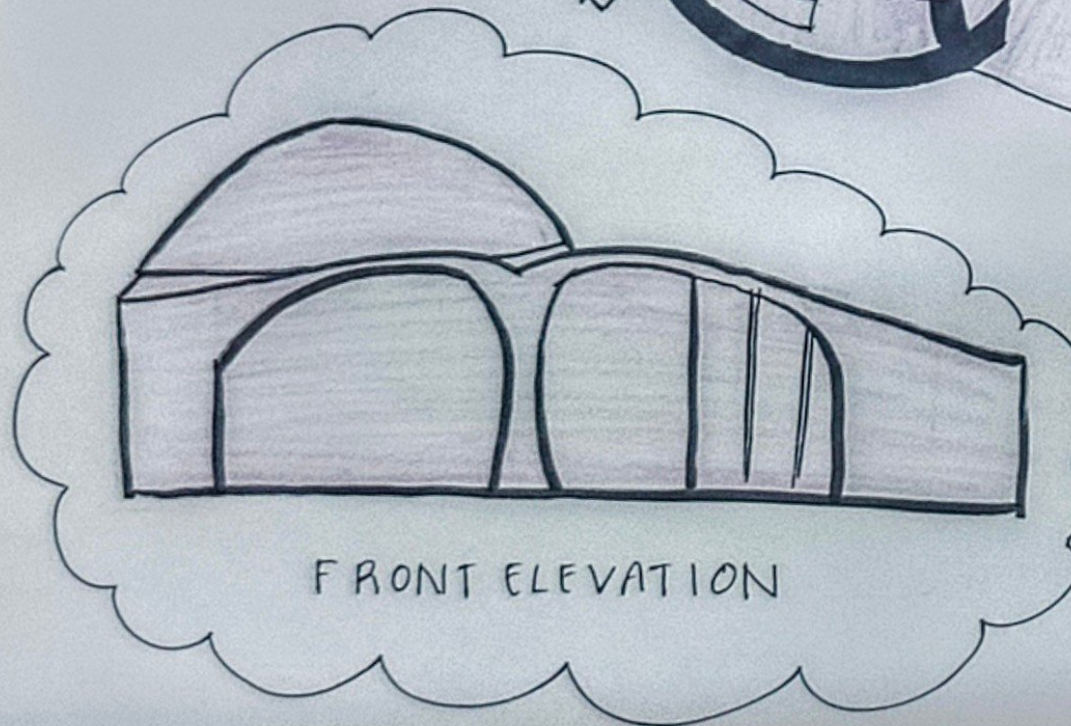

FRONT ELEVATION

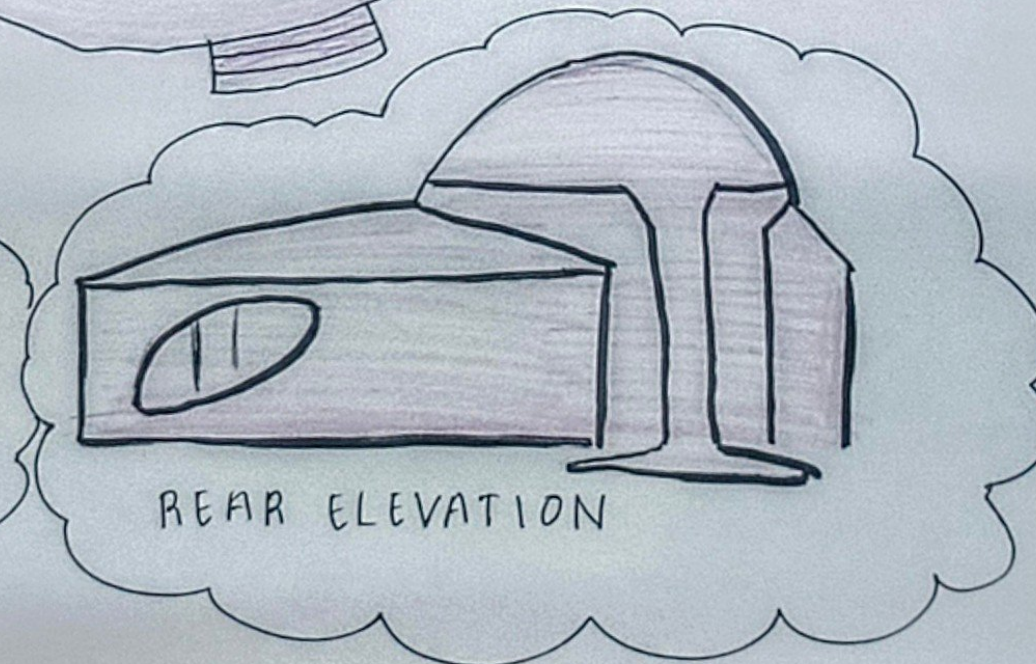

REAR ELEVATION